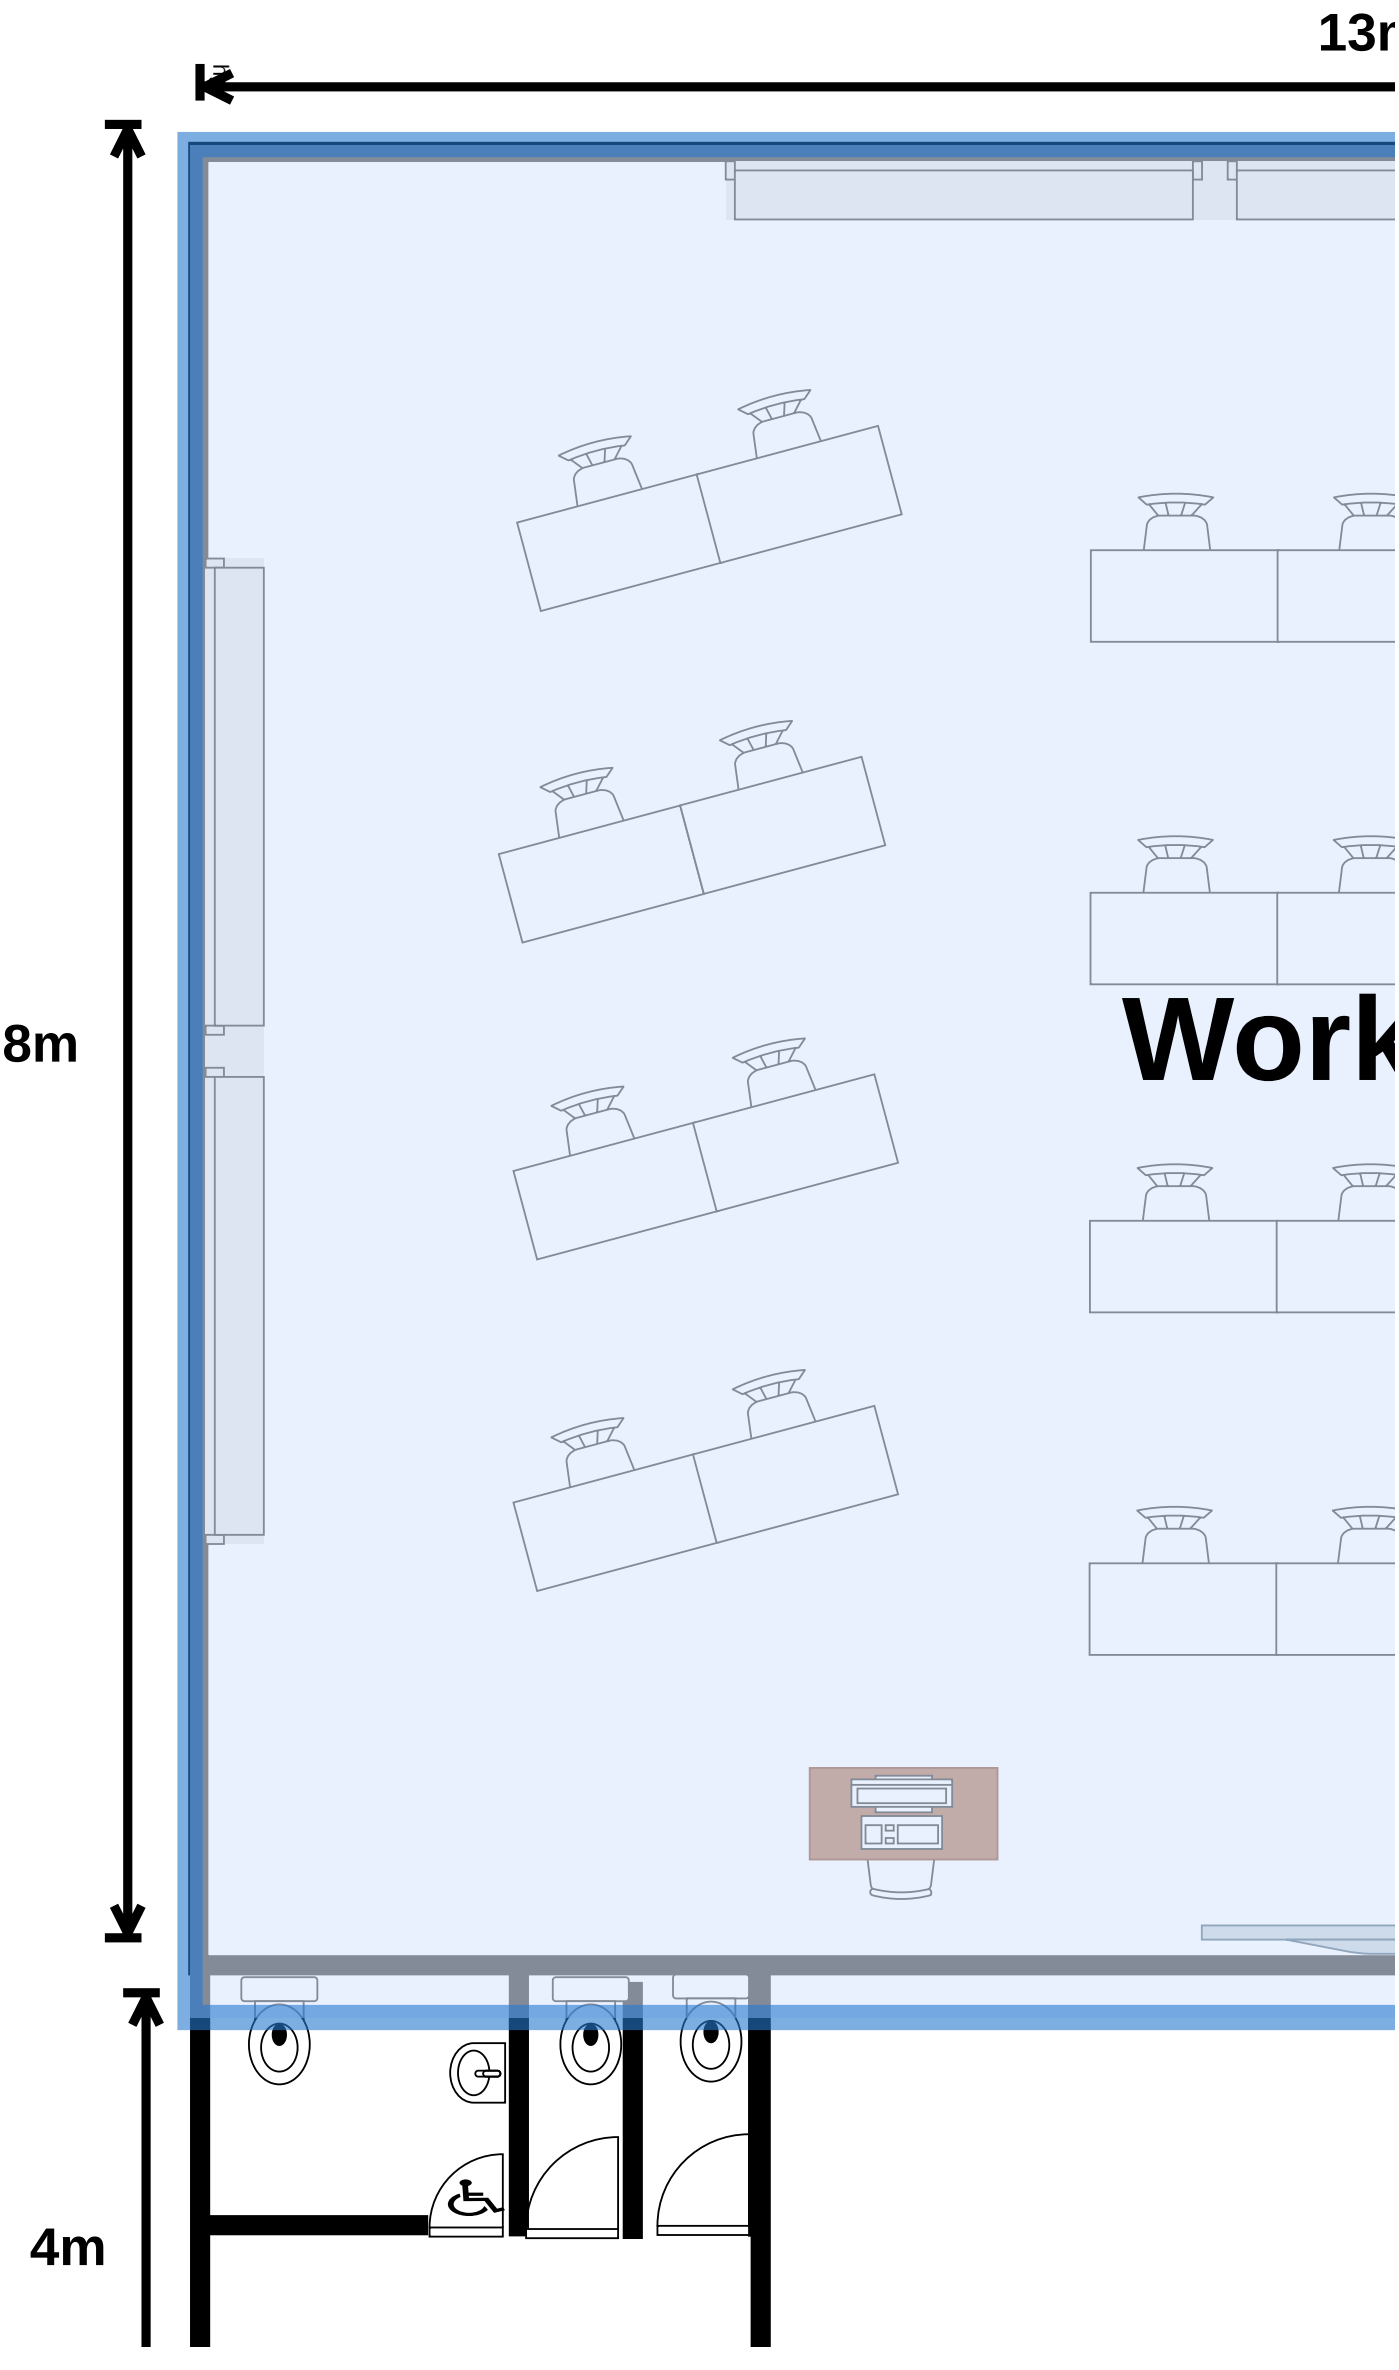
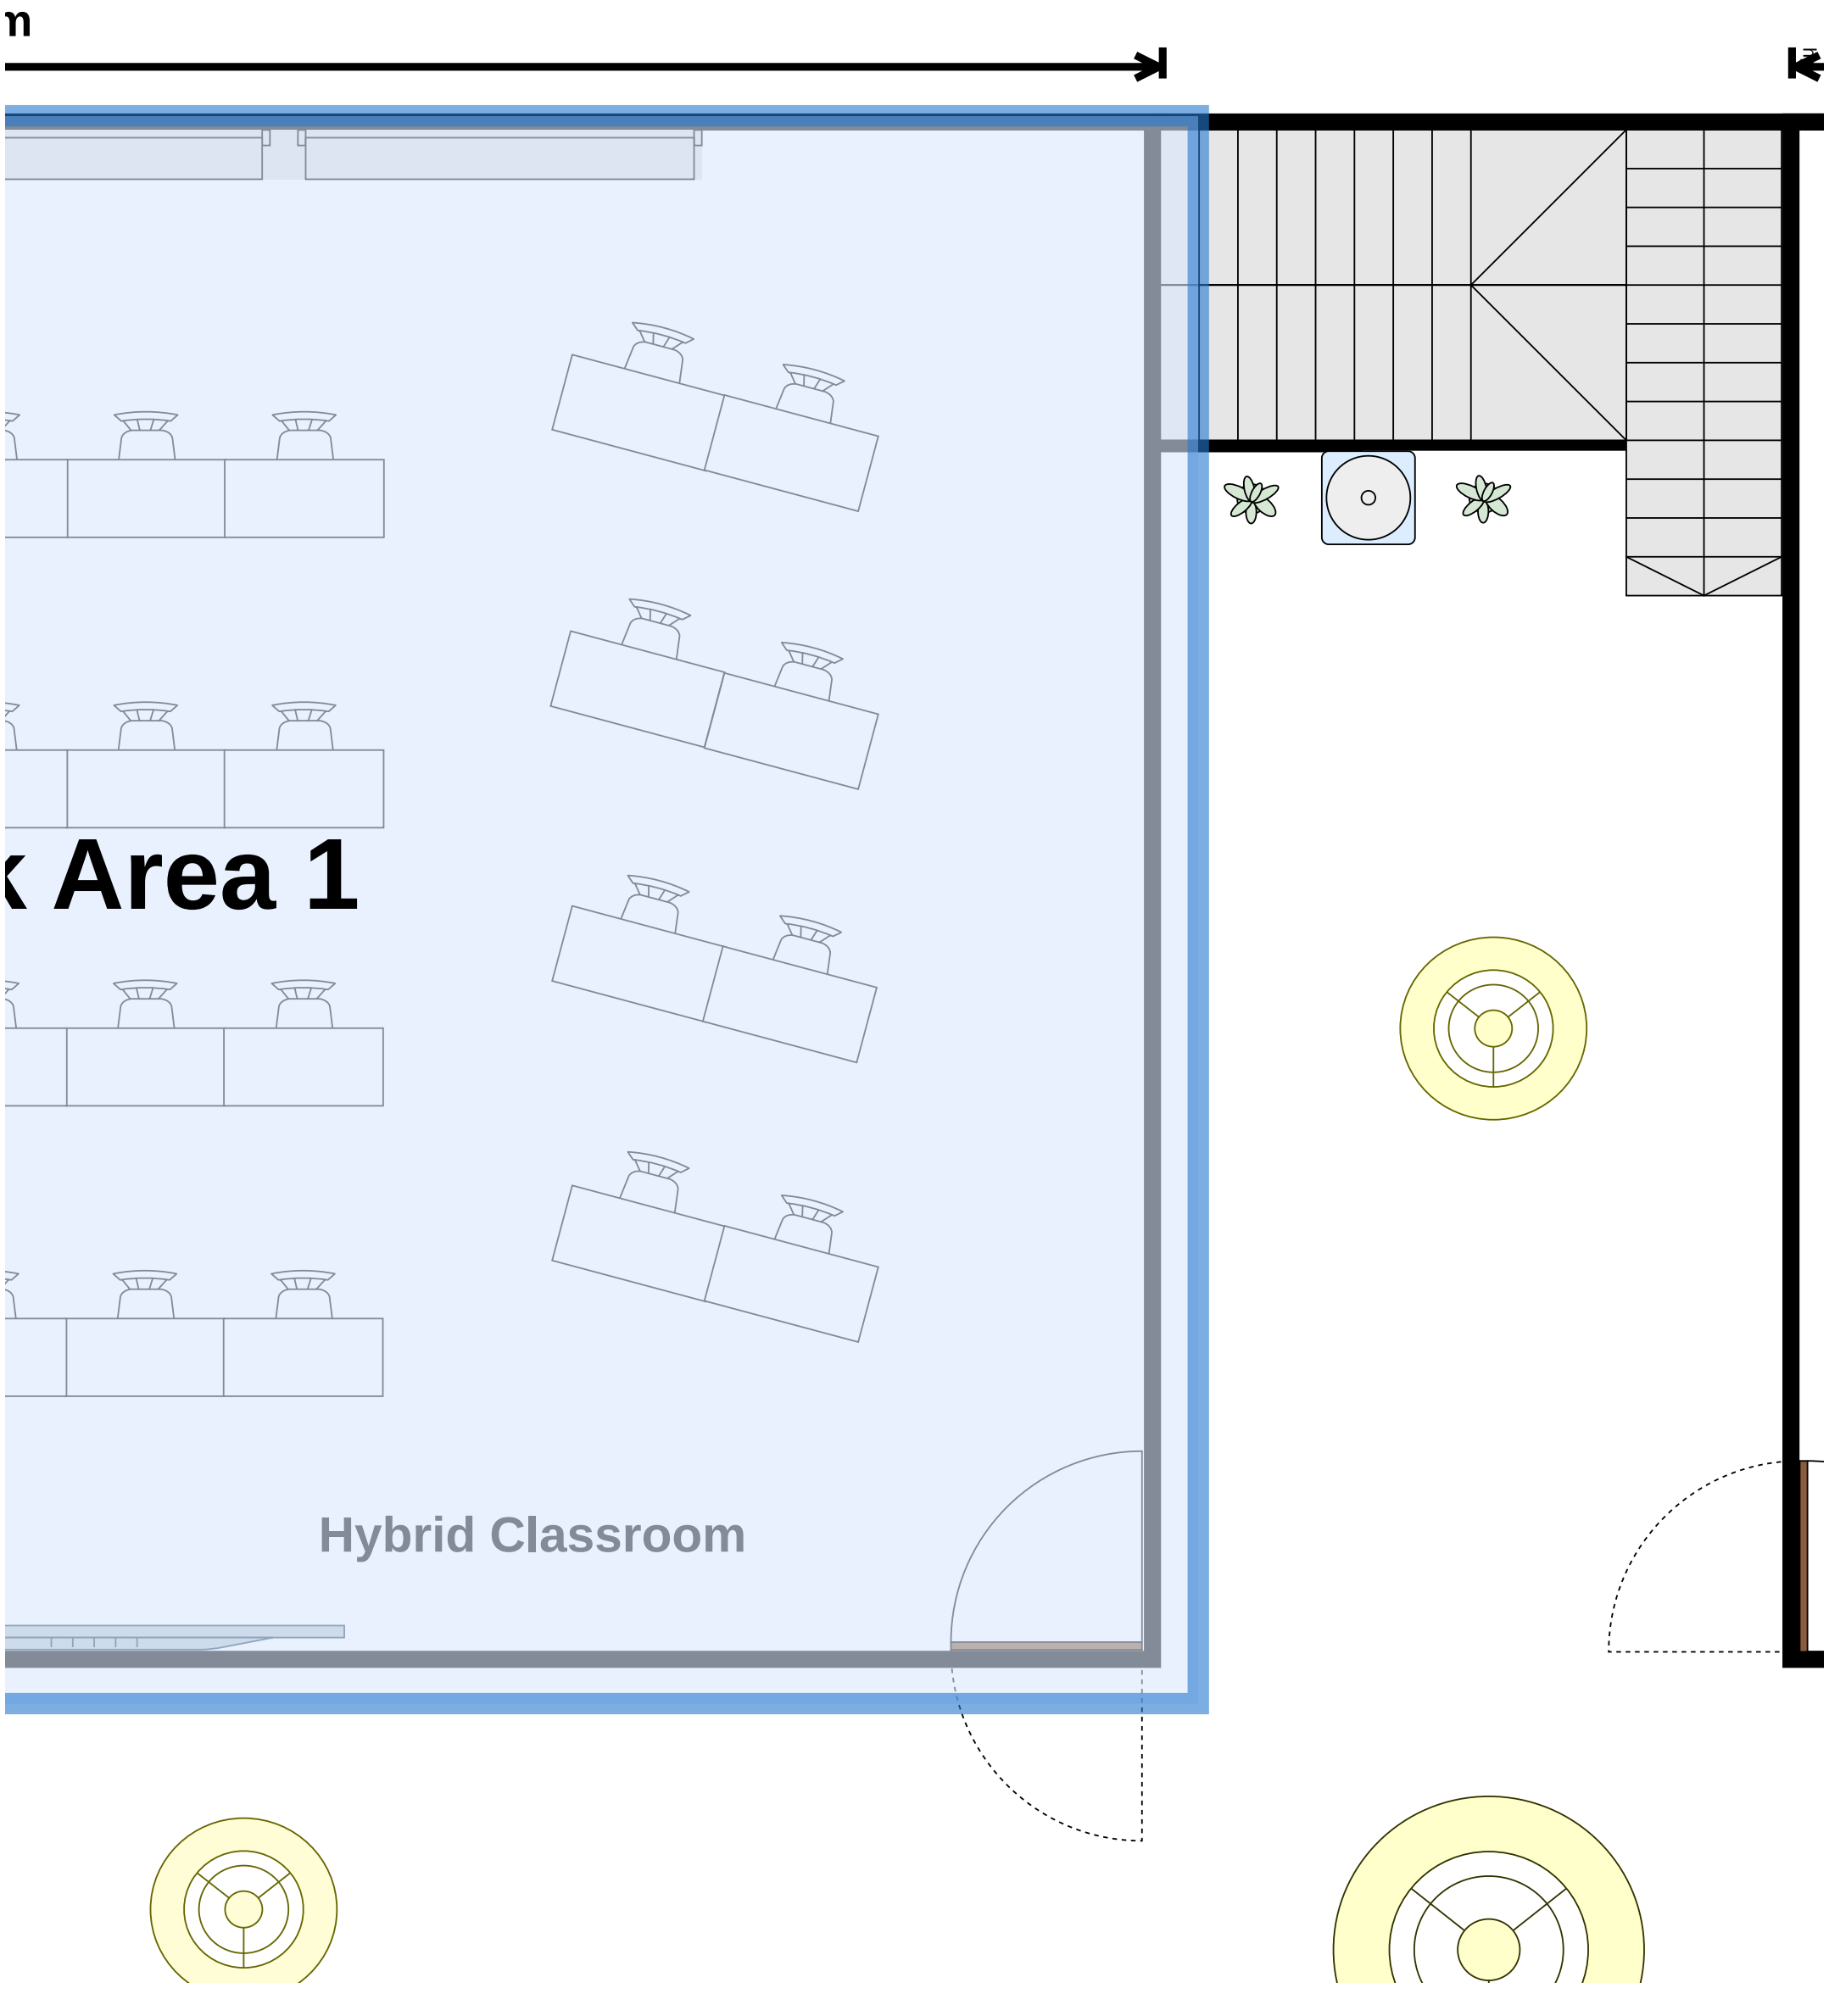
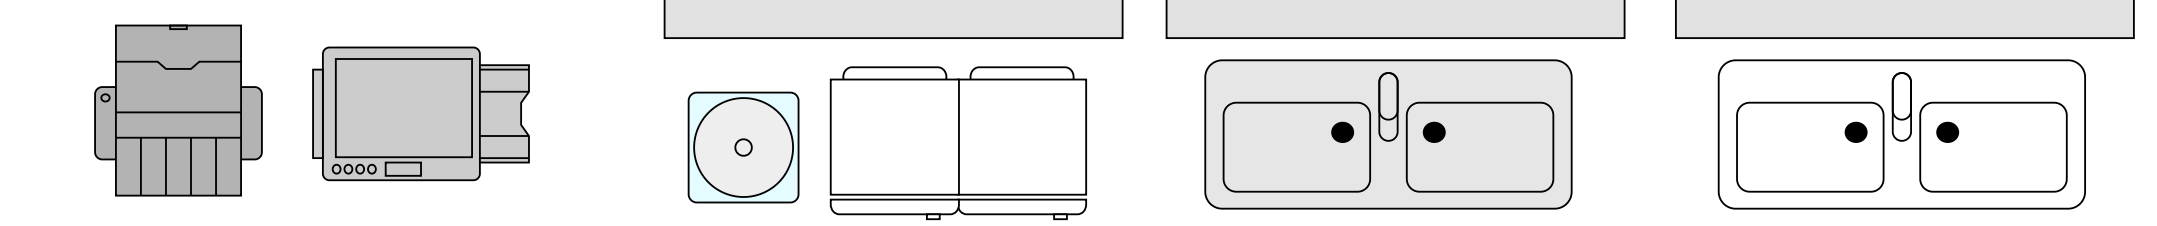
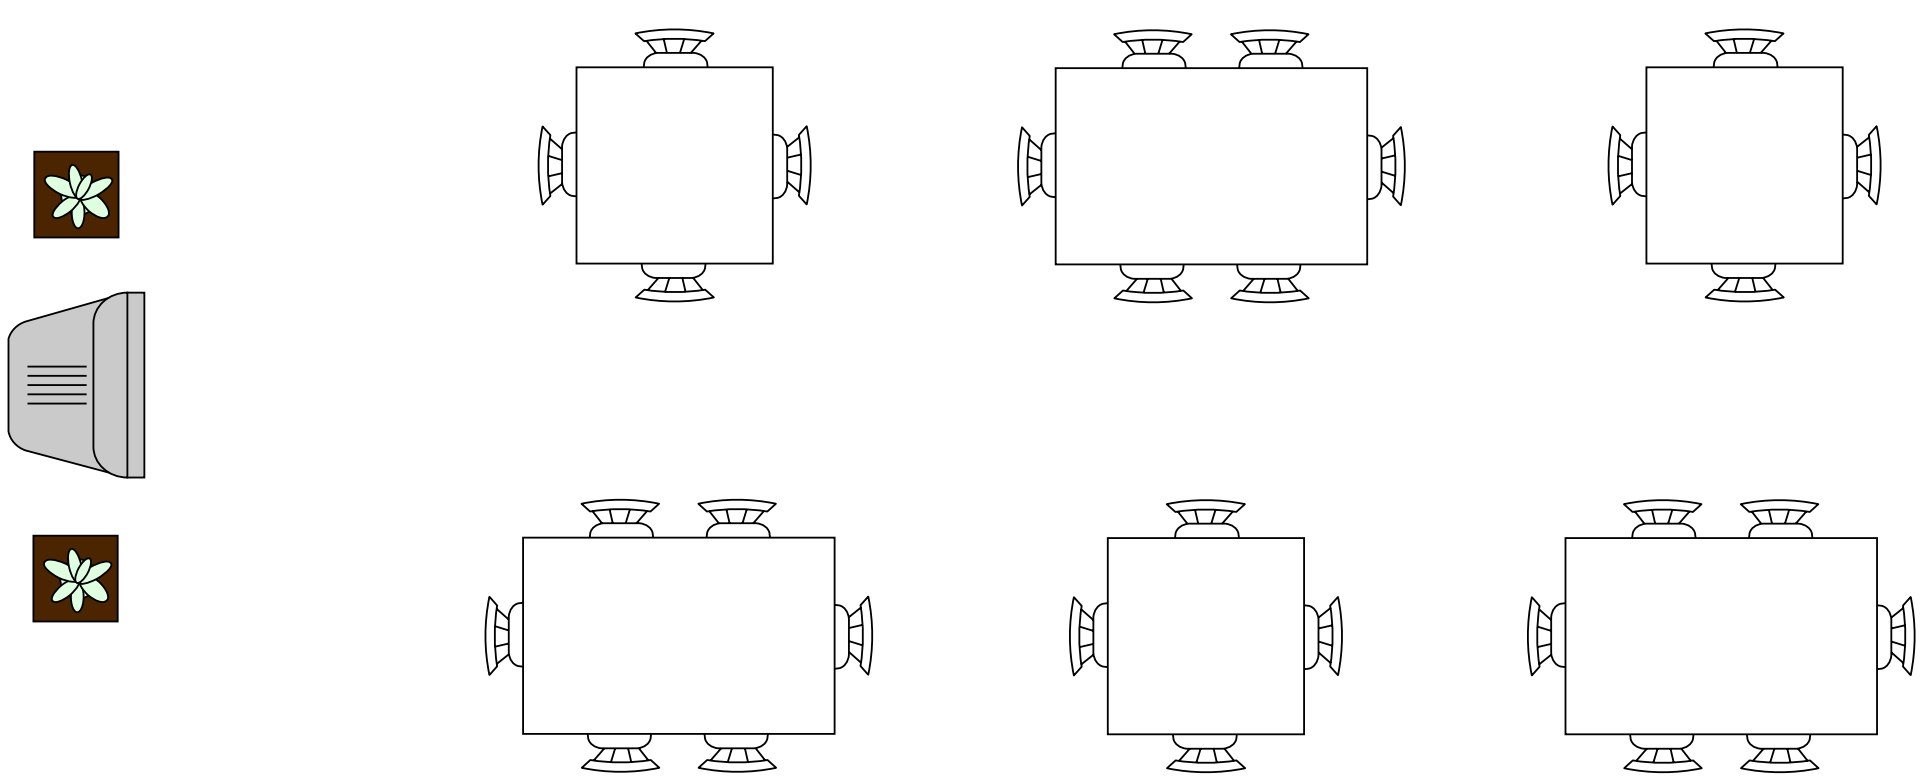

13r
8m
Work
4m

First Floor

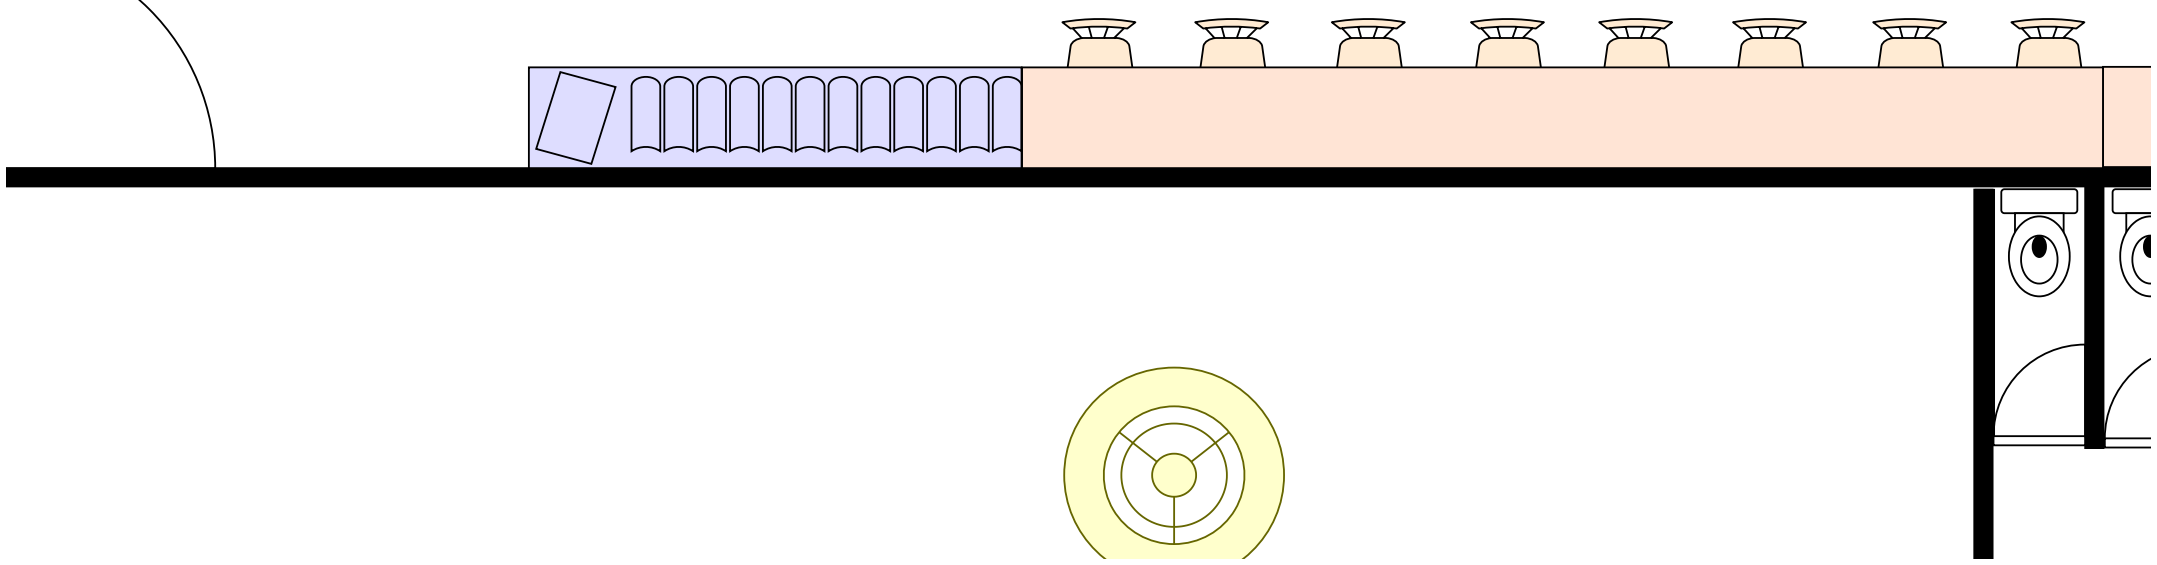


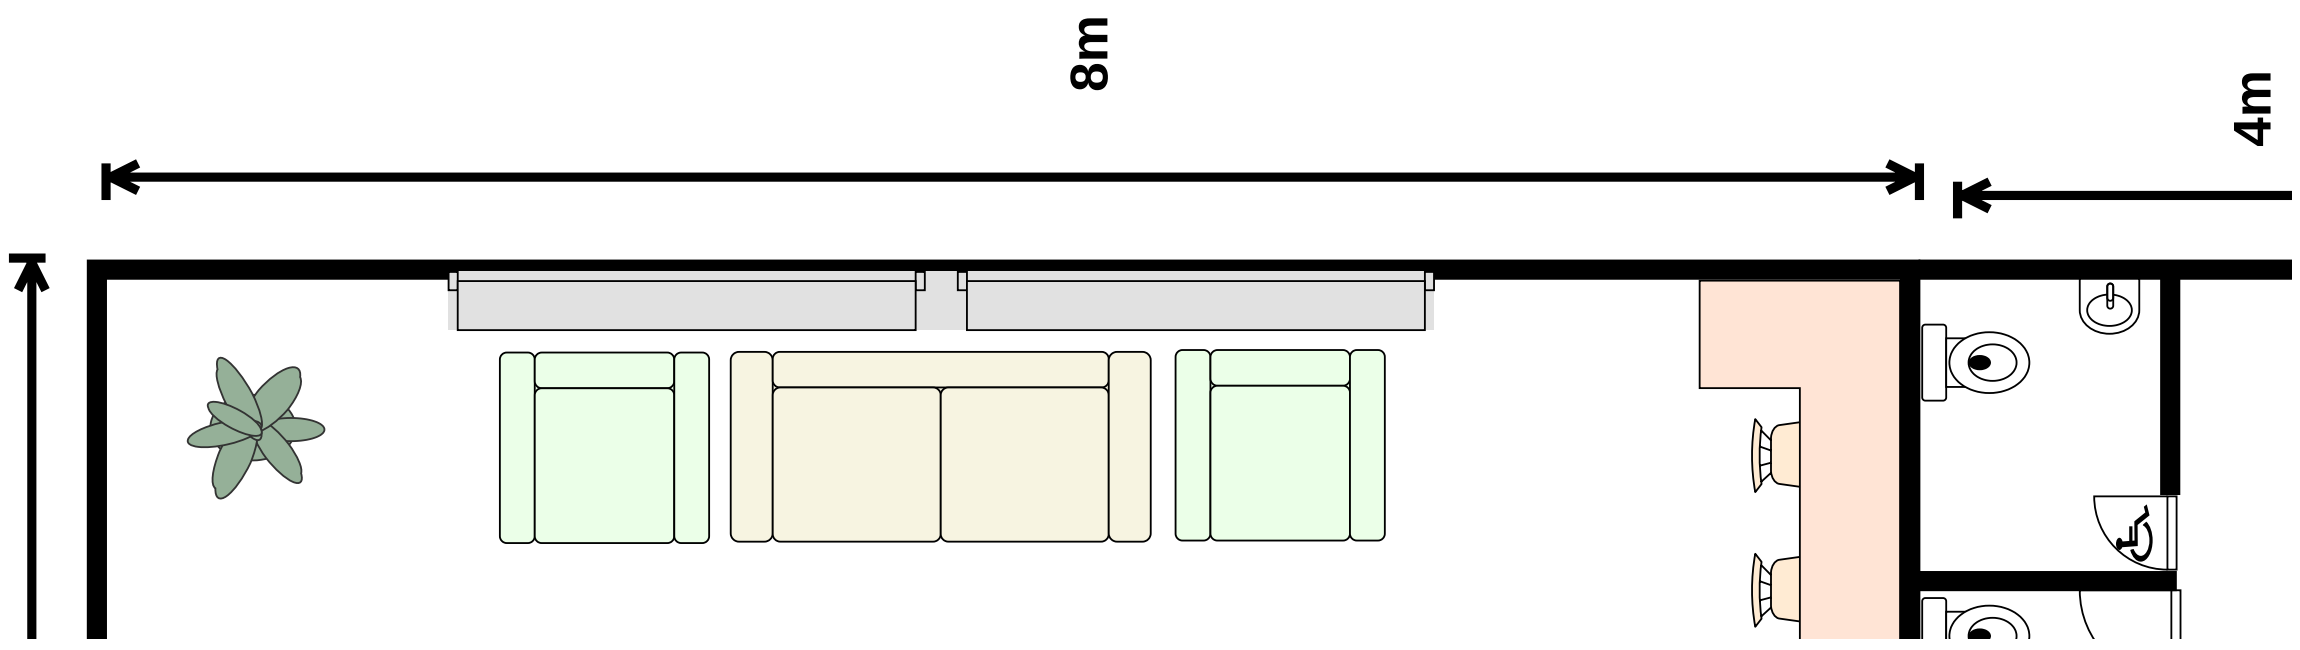
13m

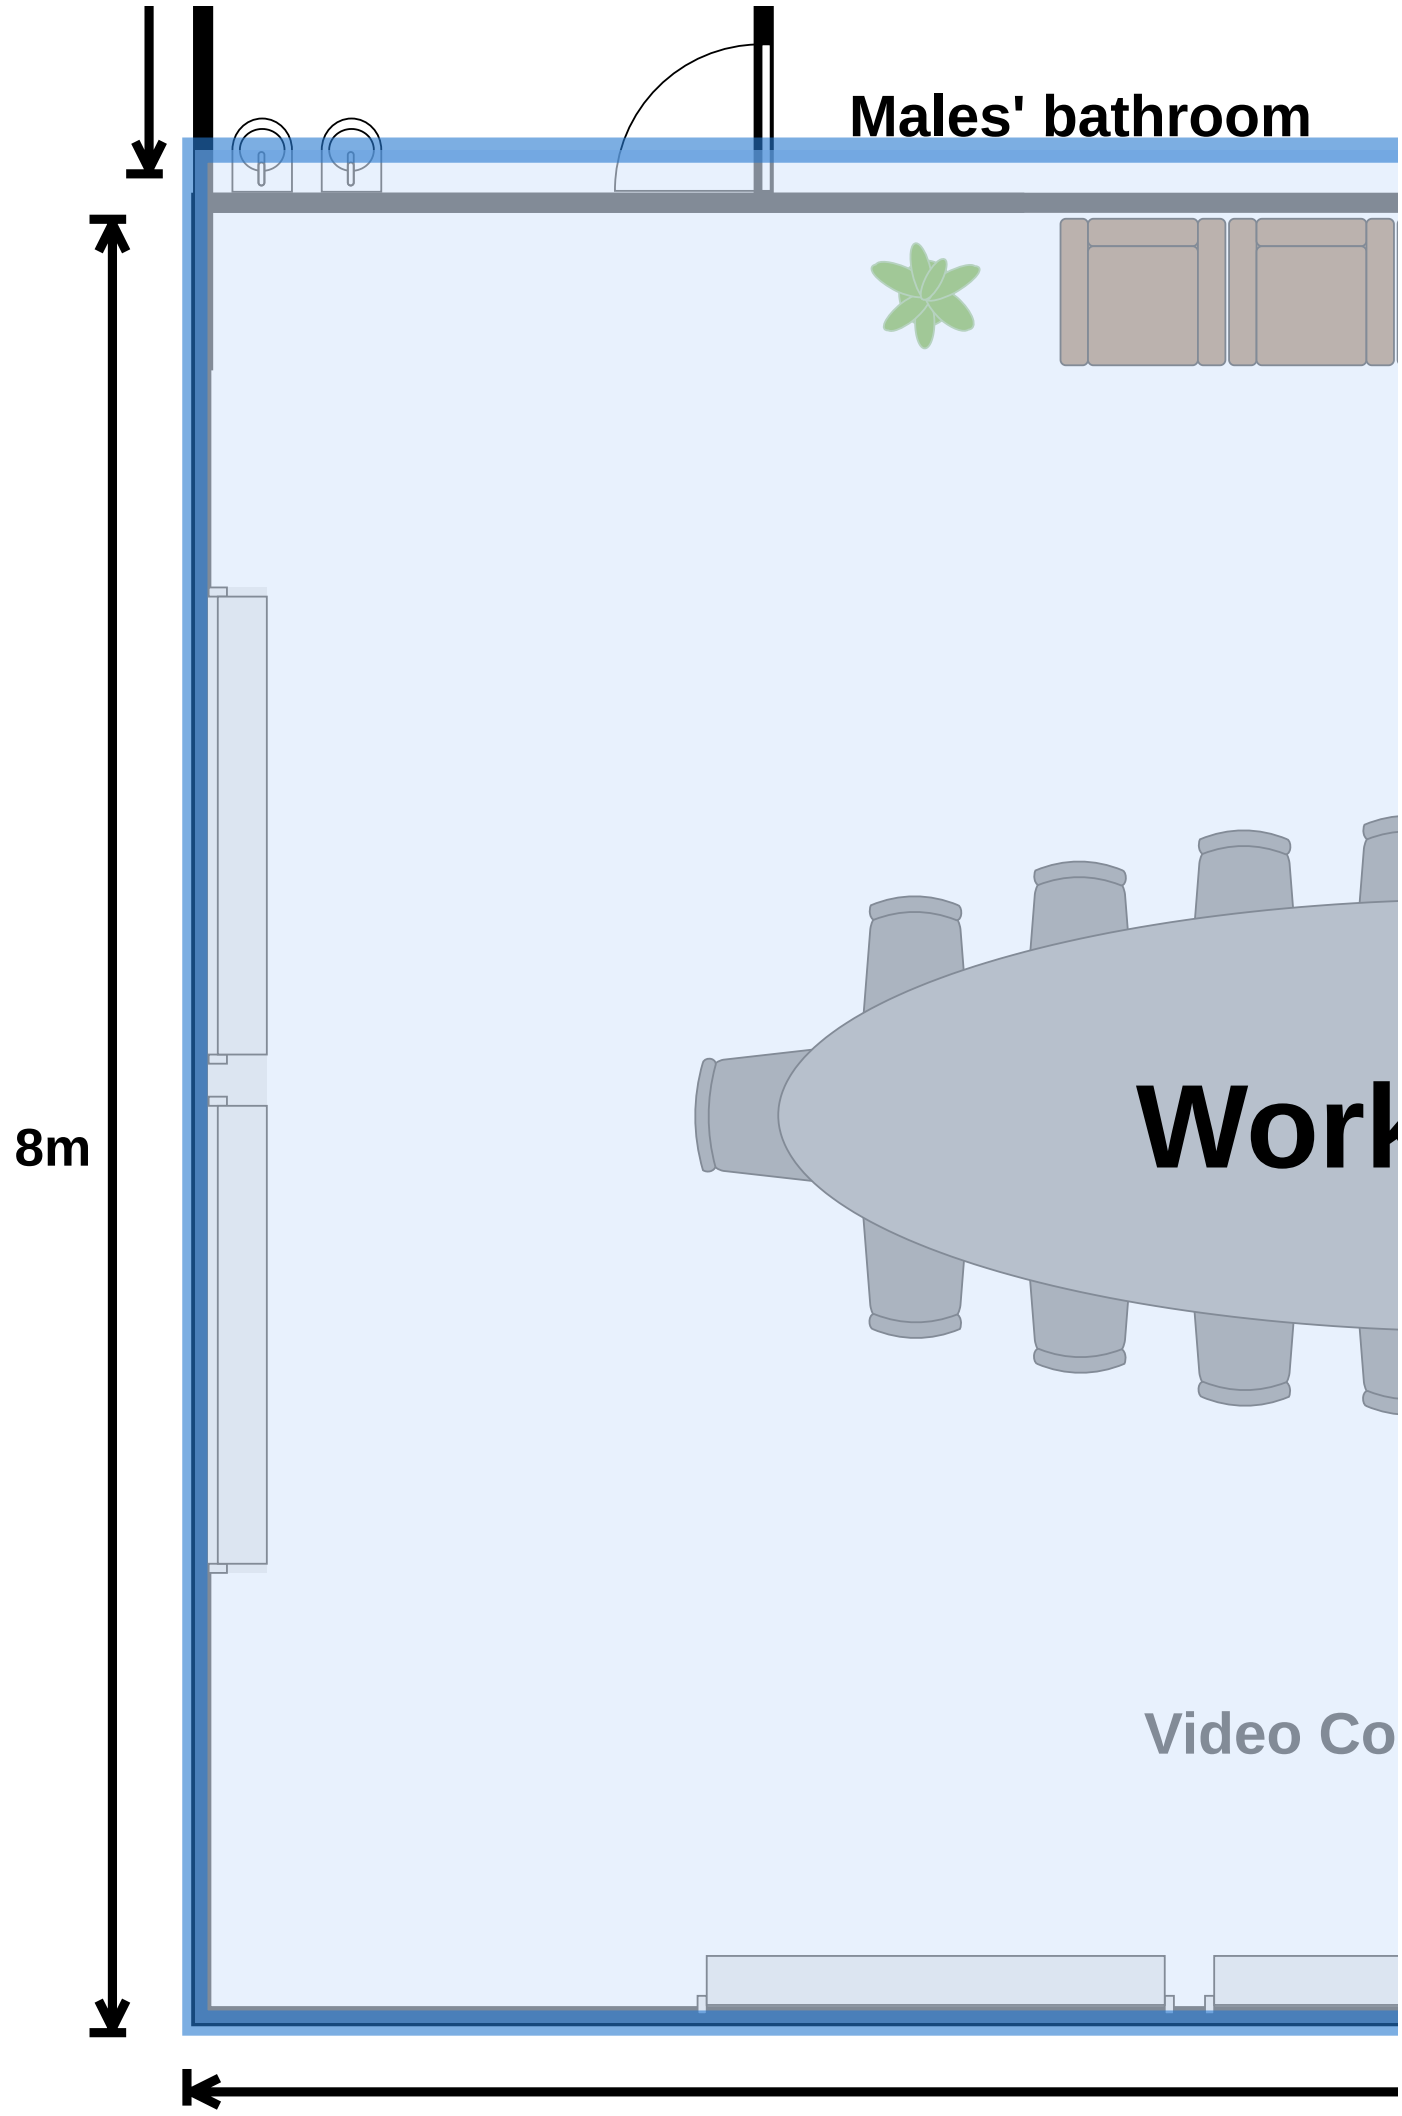


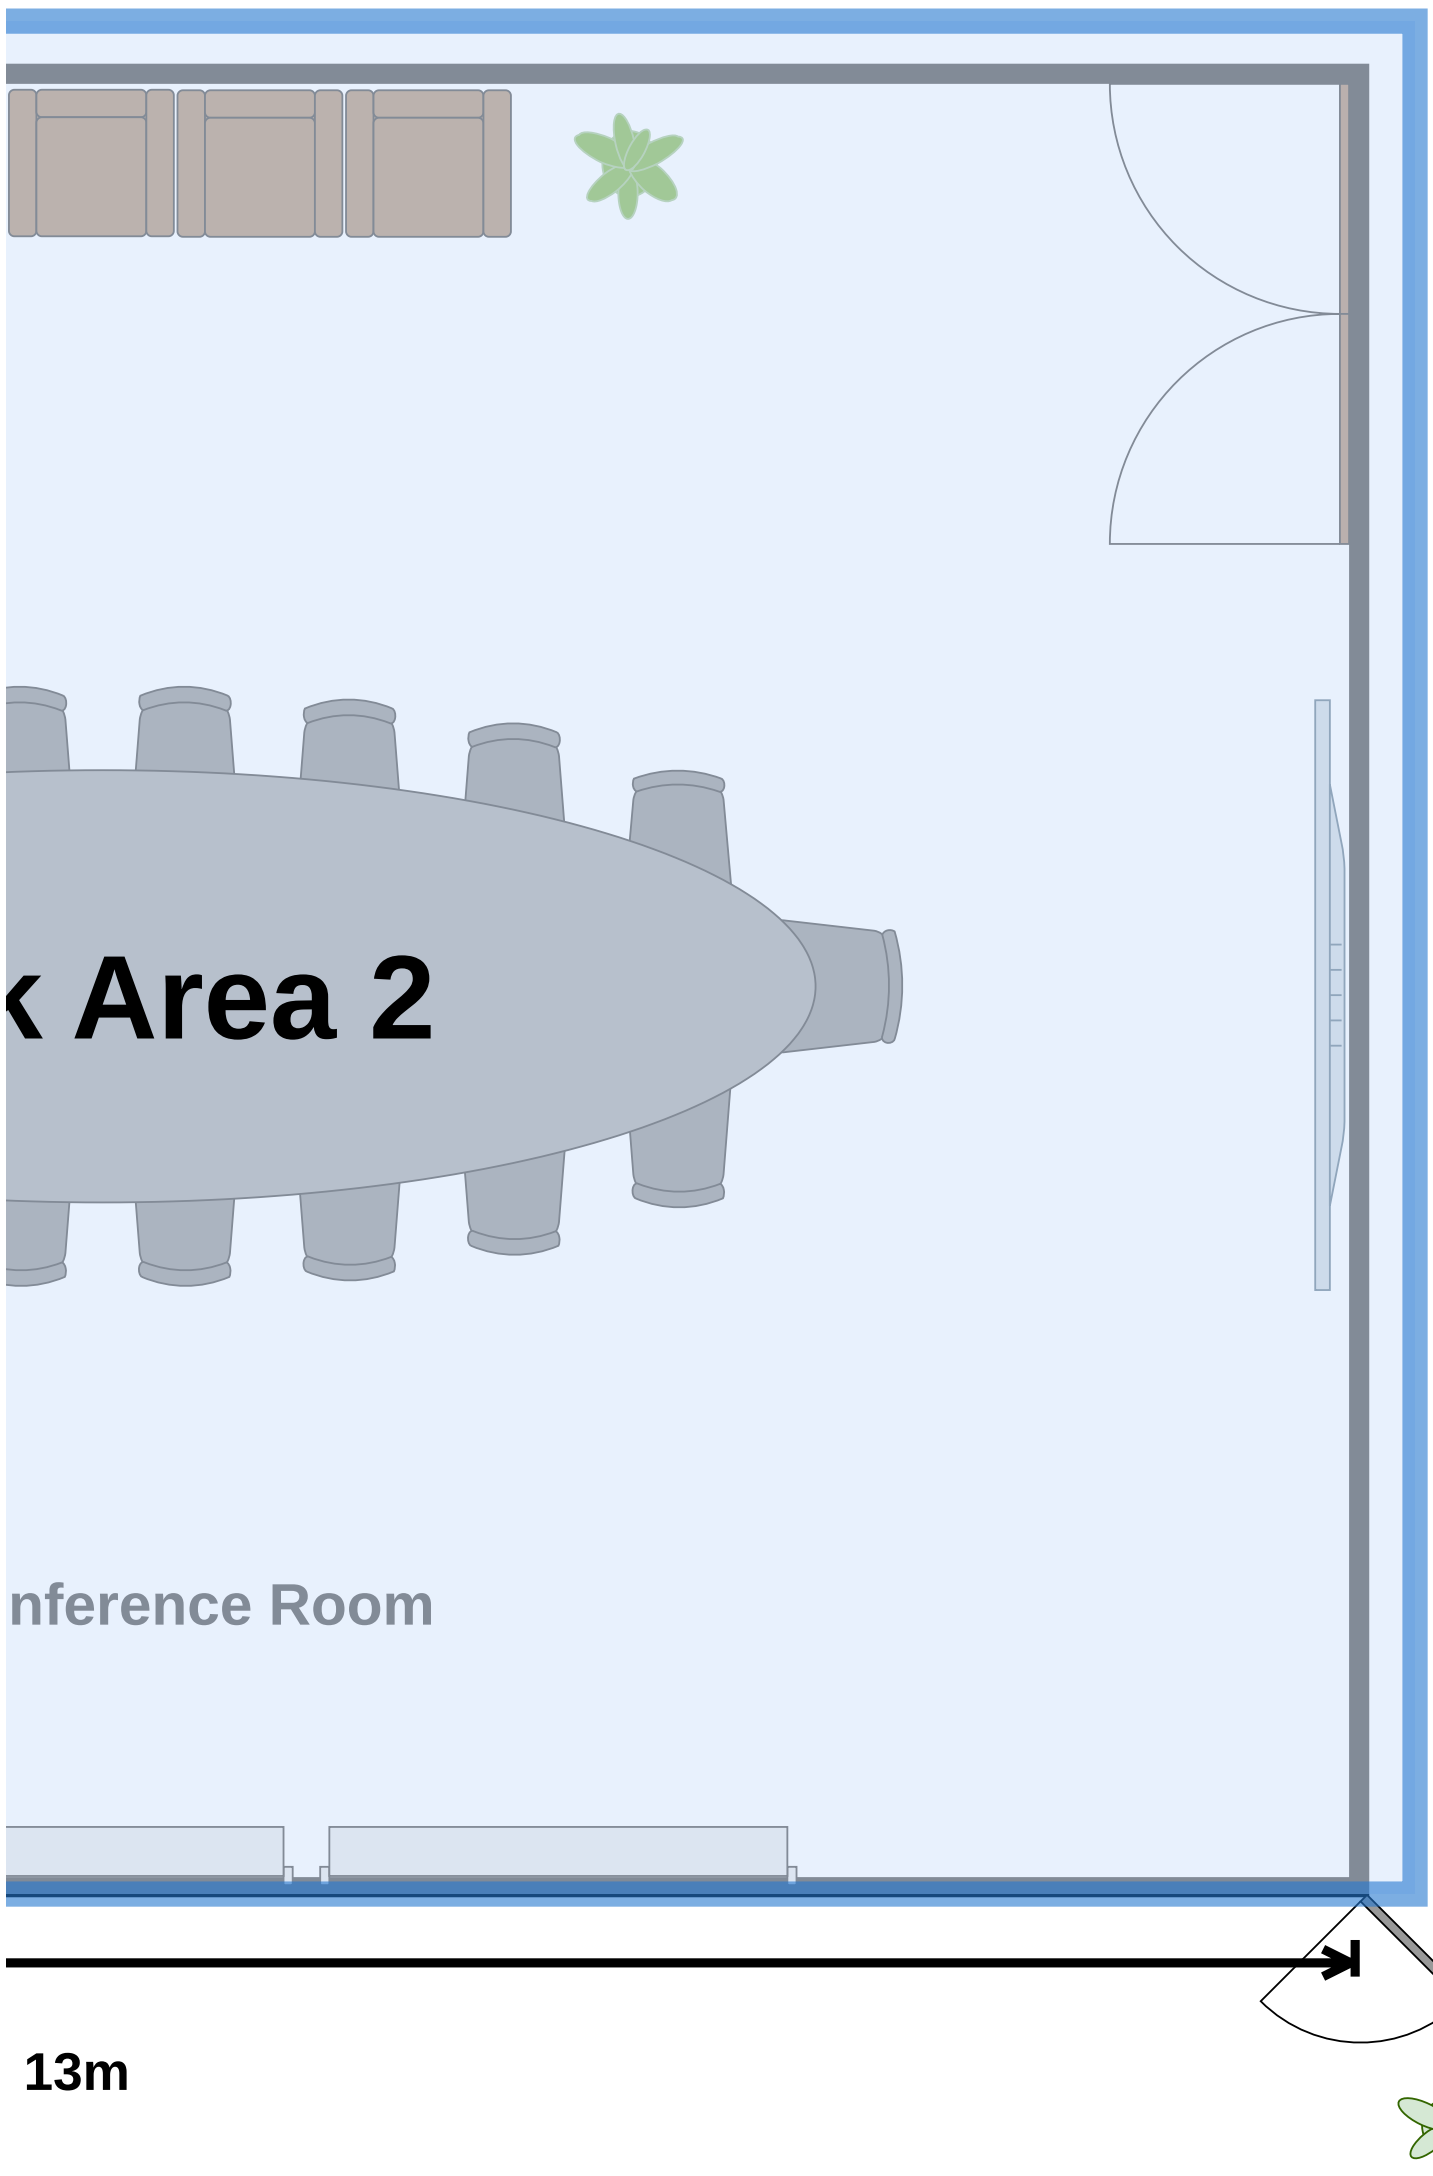


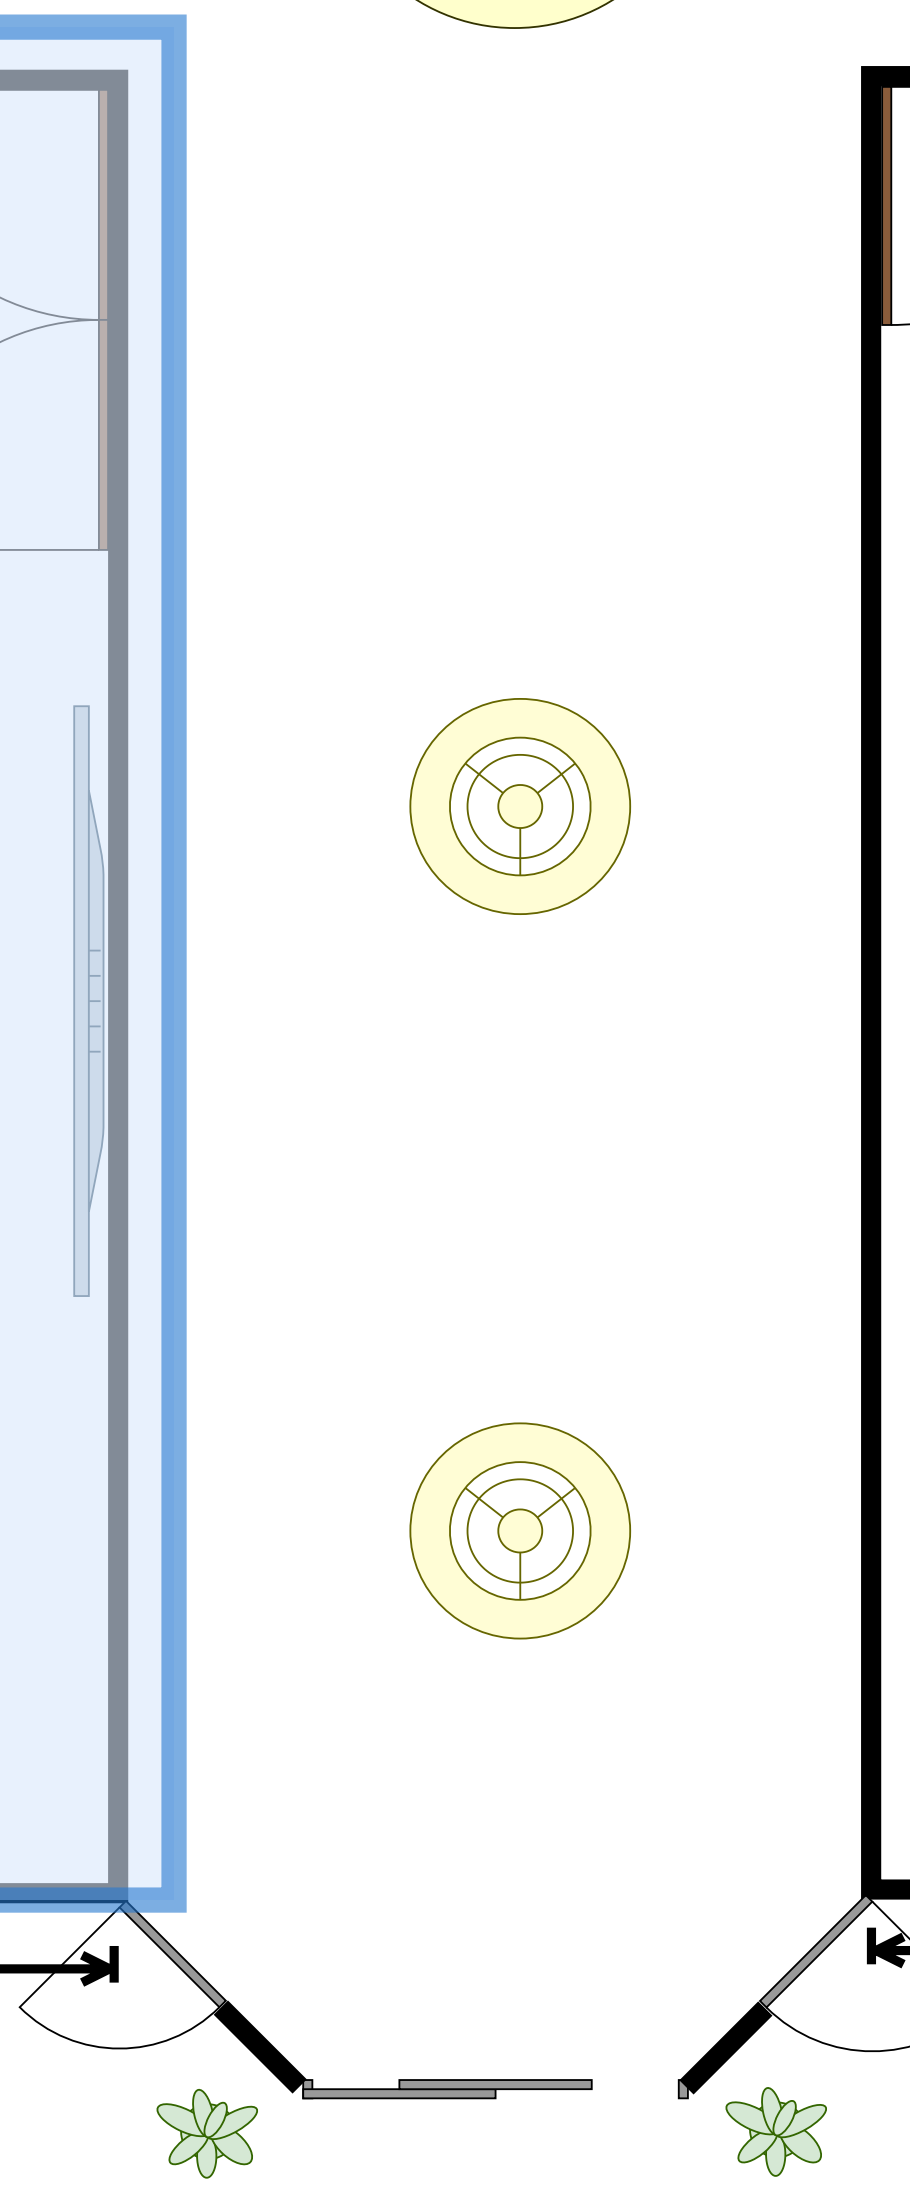
Student Lounge




8m
4m


Males' bathroom
Work
Video Co
8m





13m

Second Floor

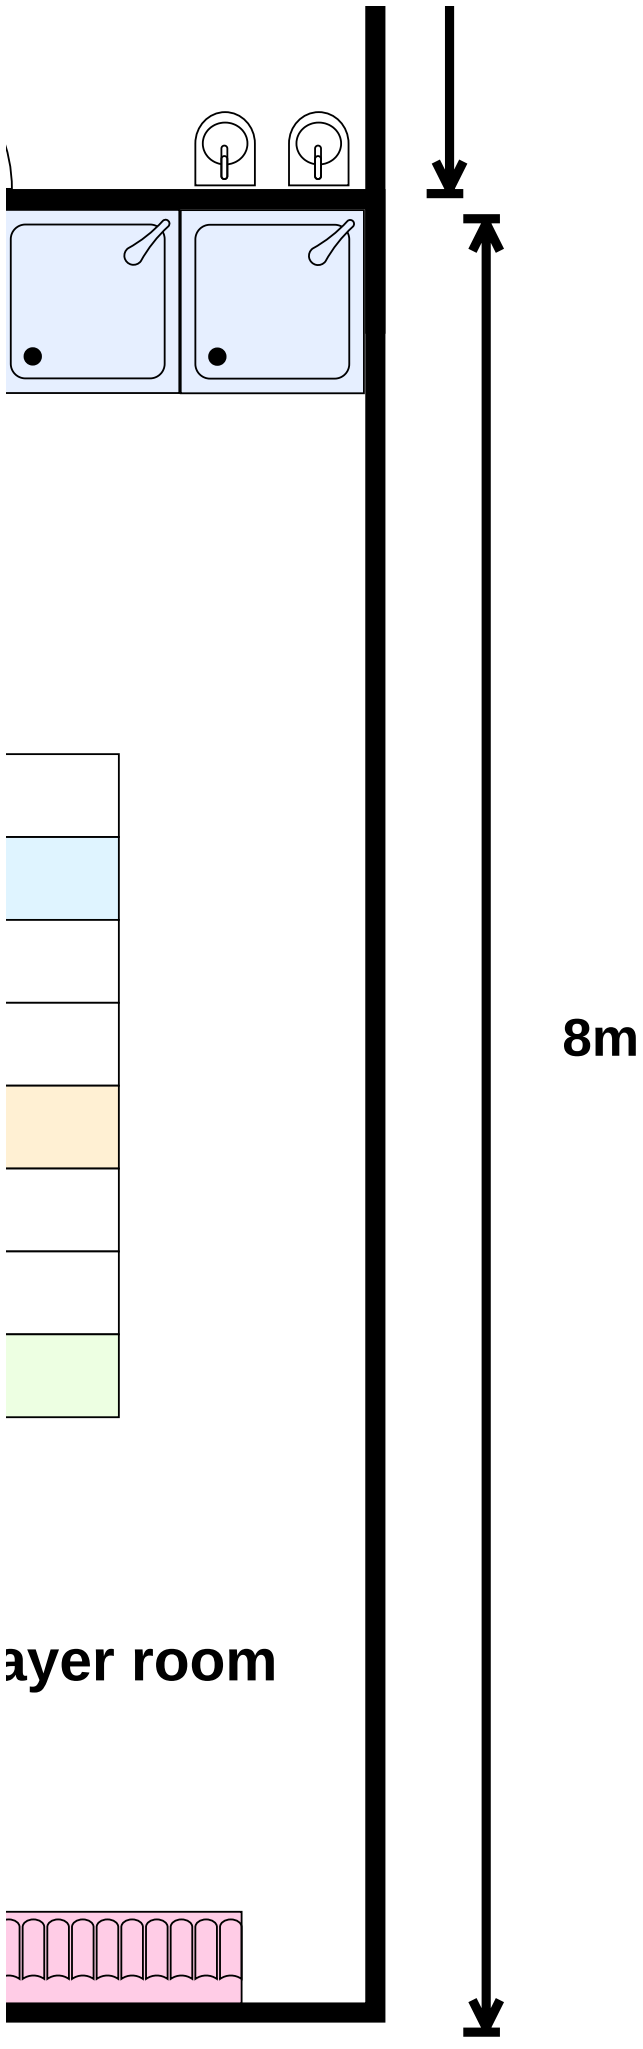
Females' bathroom

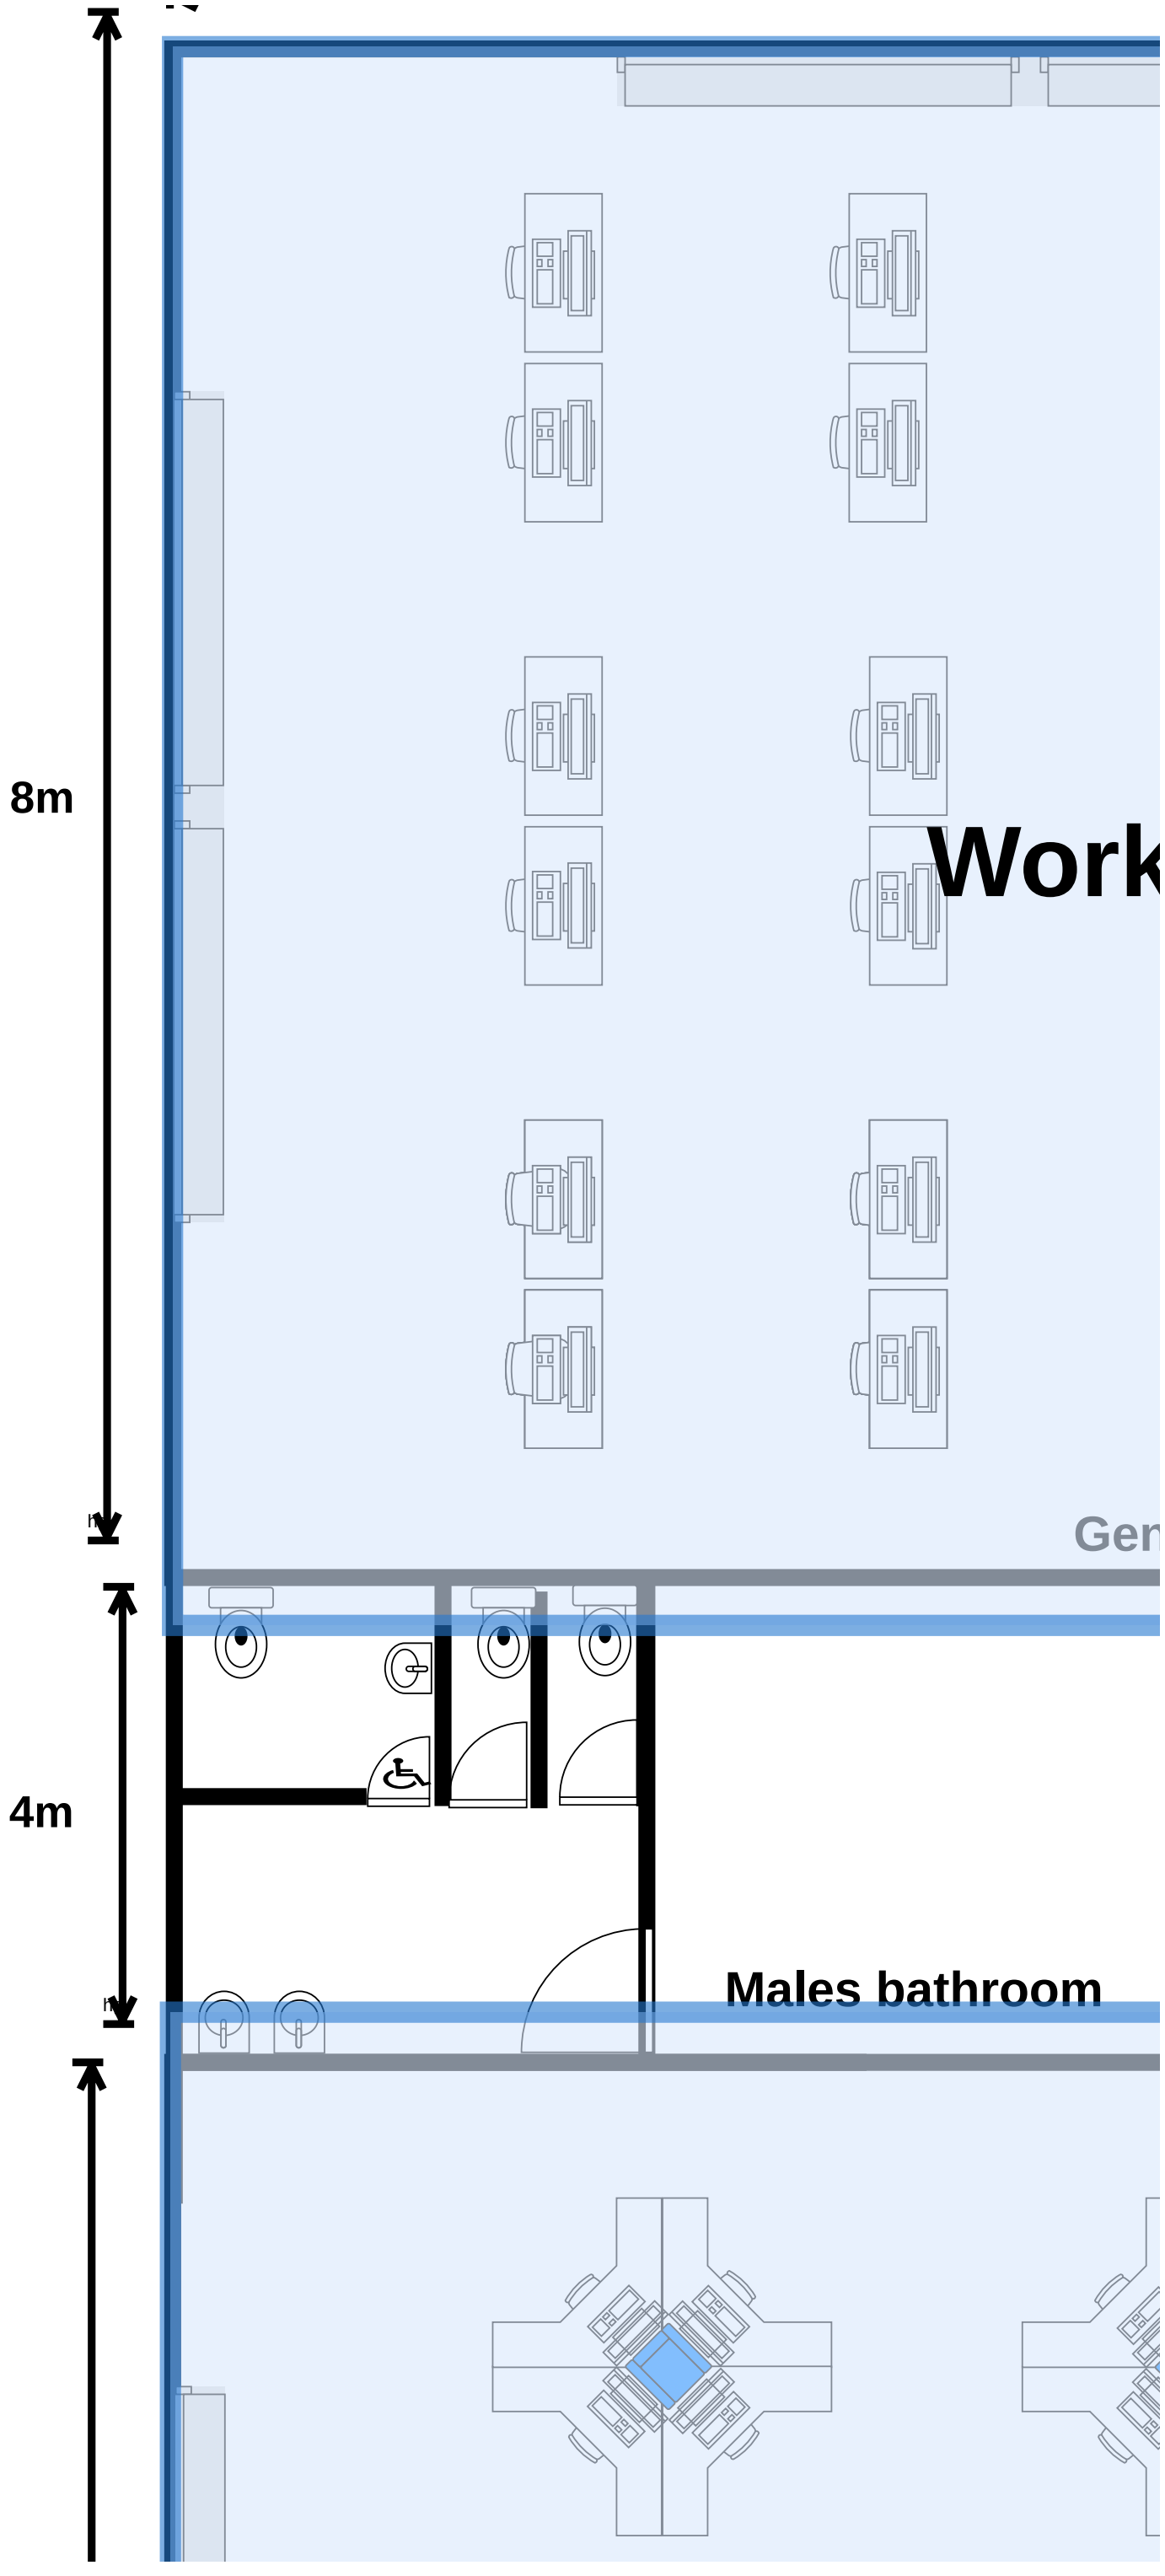
Males' prayer room

Females' pra

13m

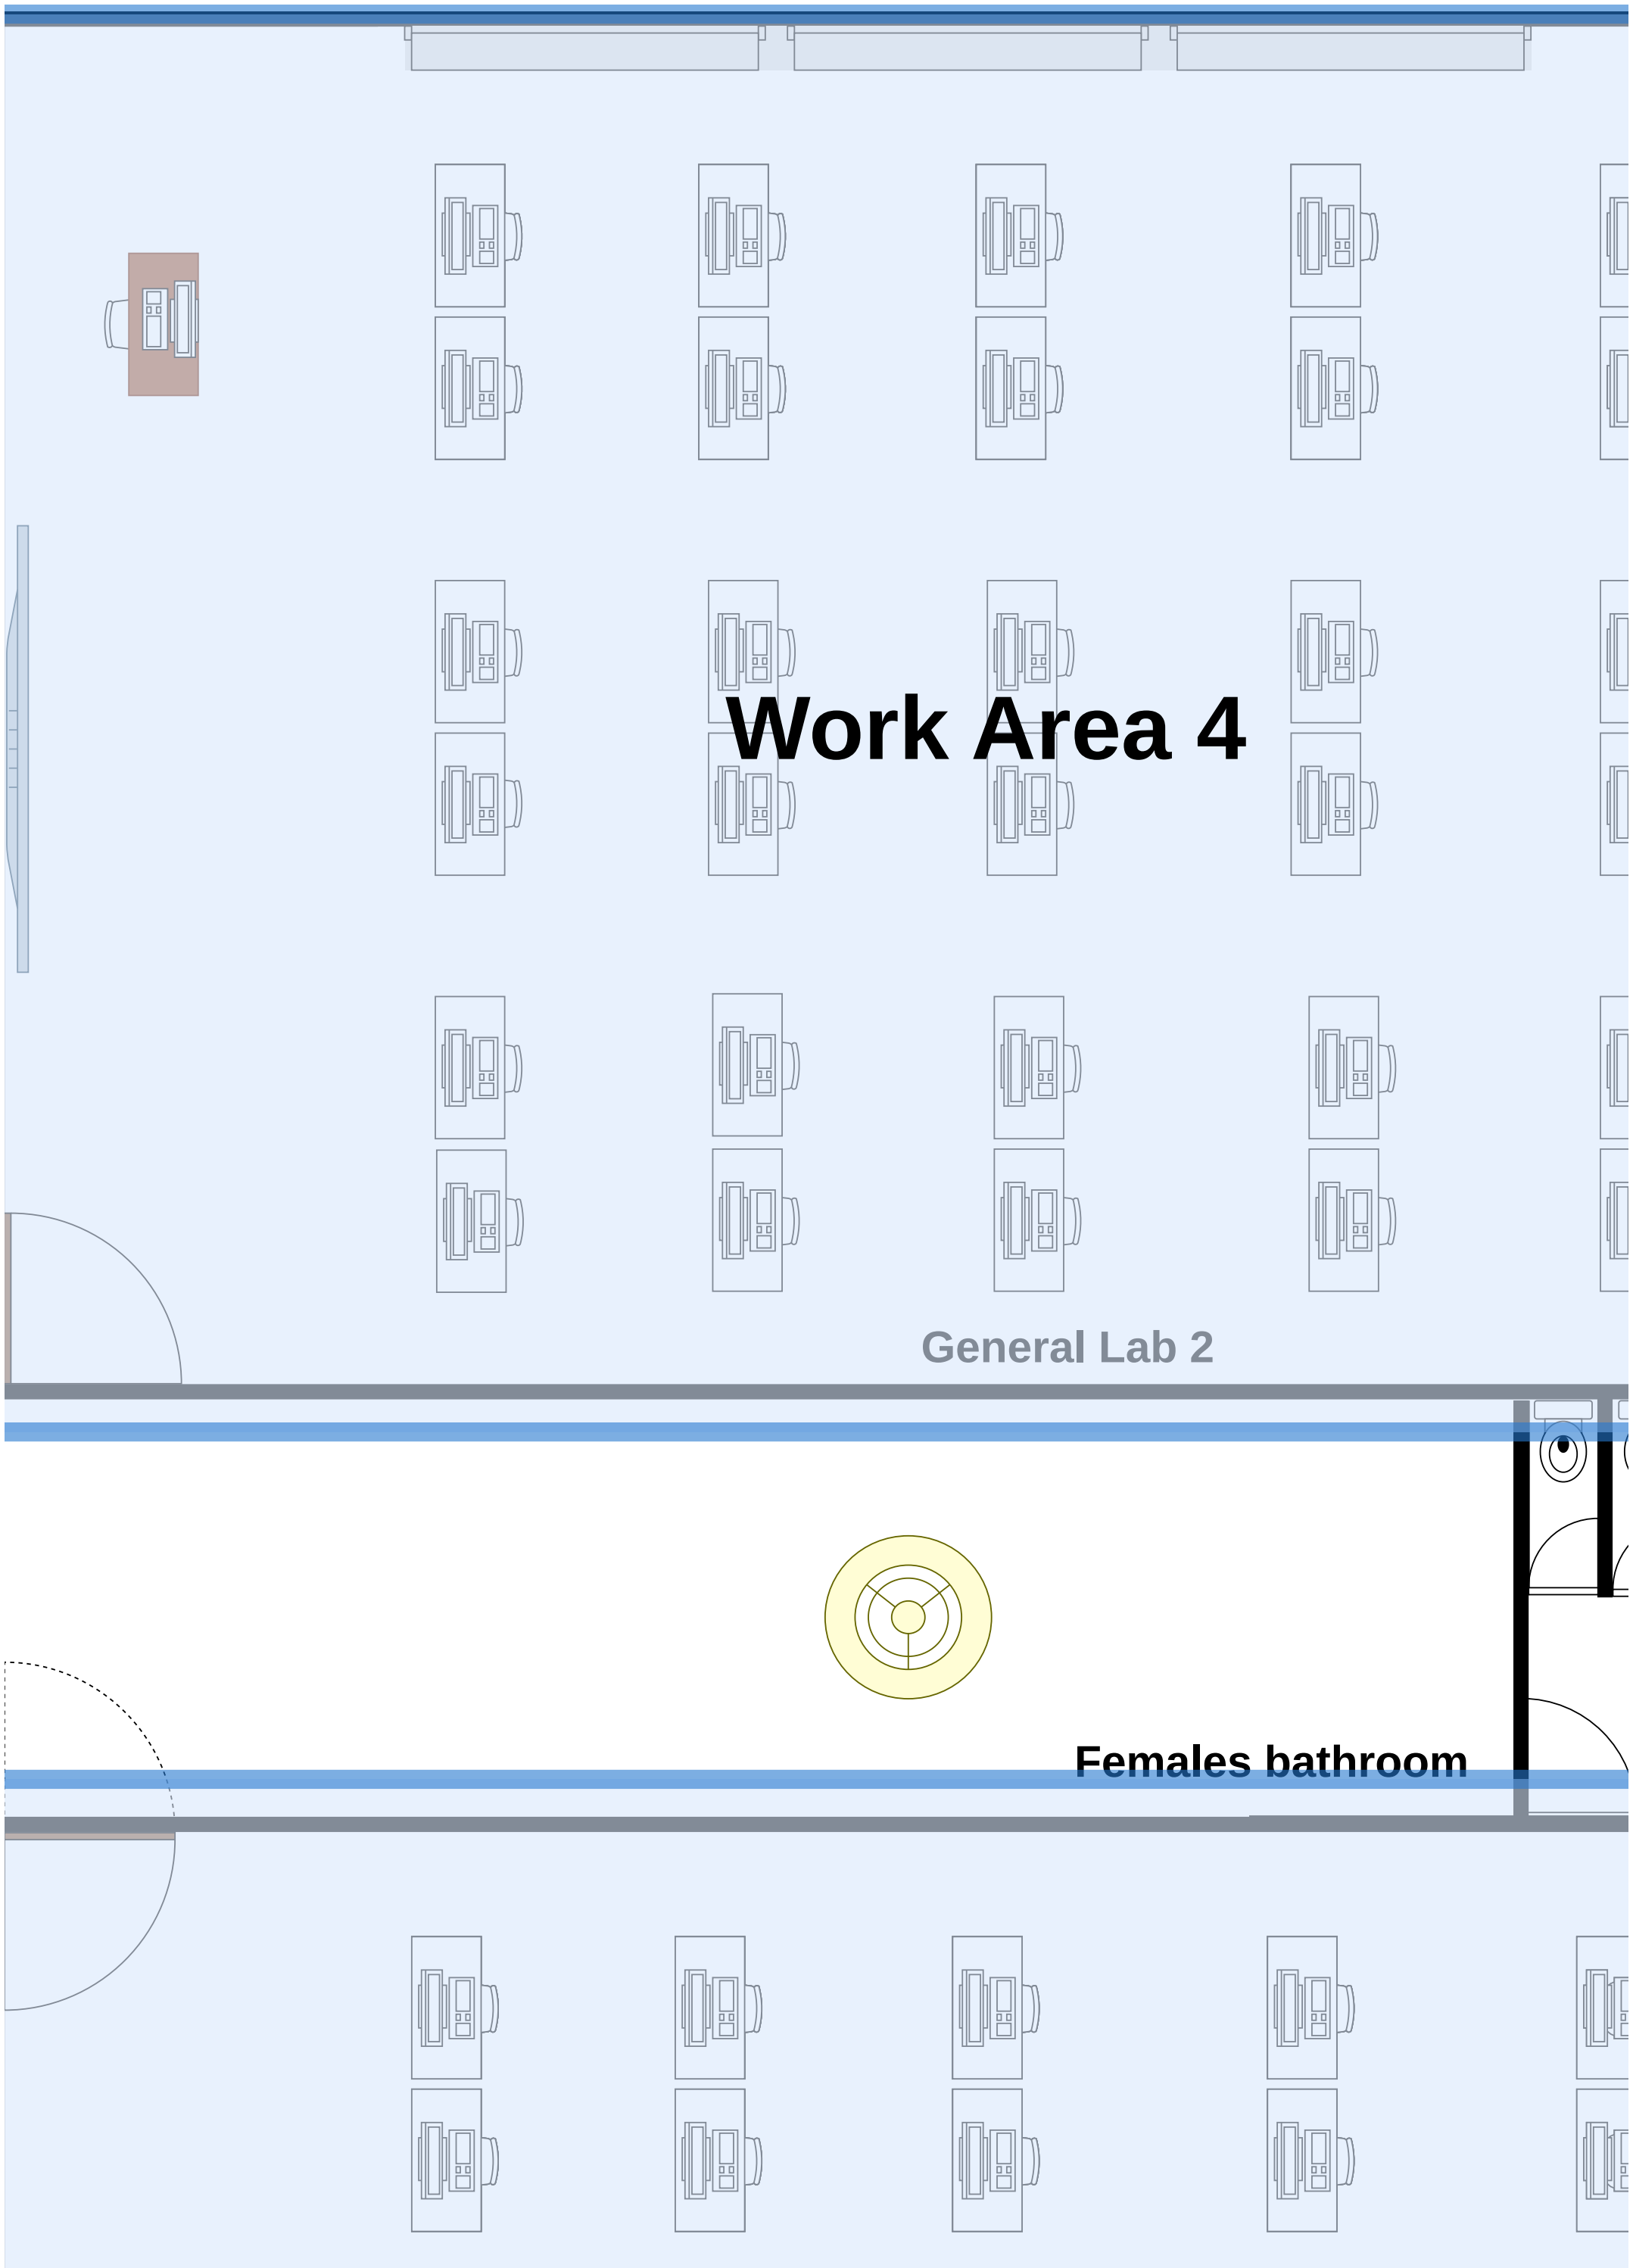
13m

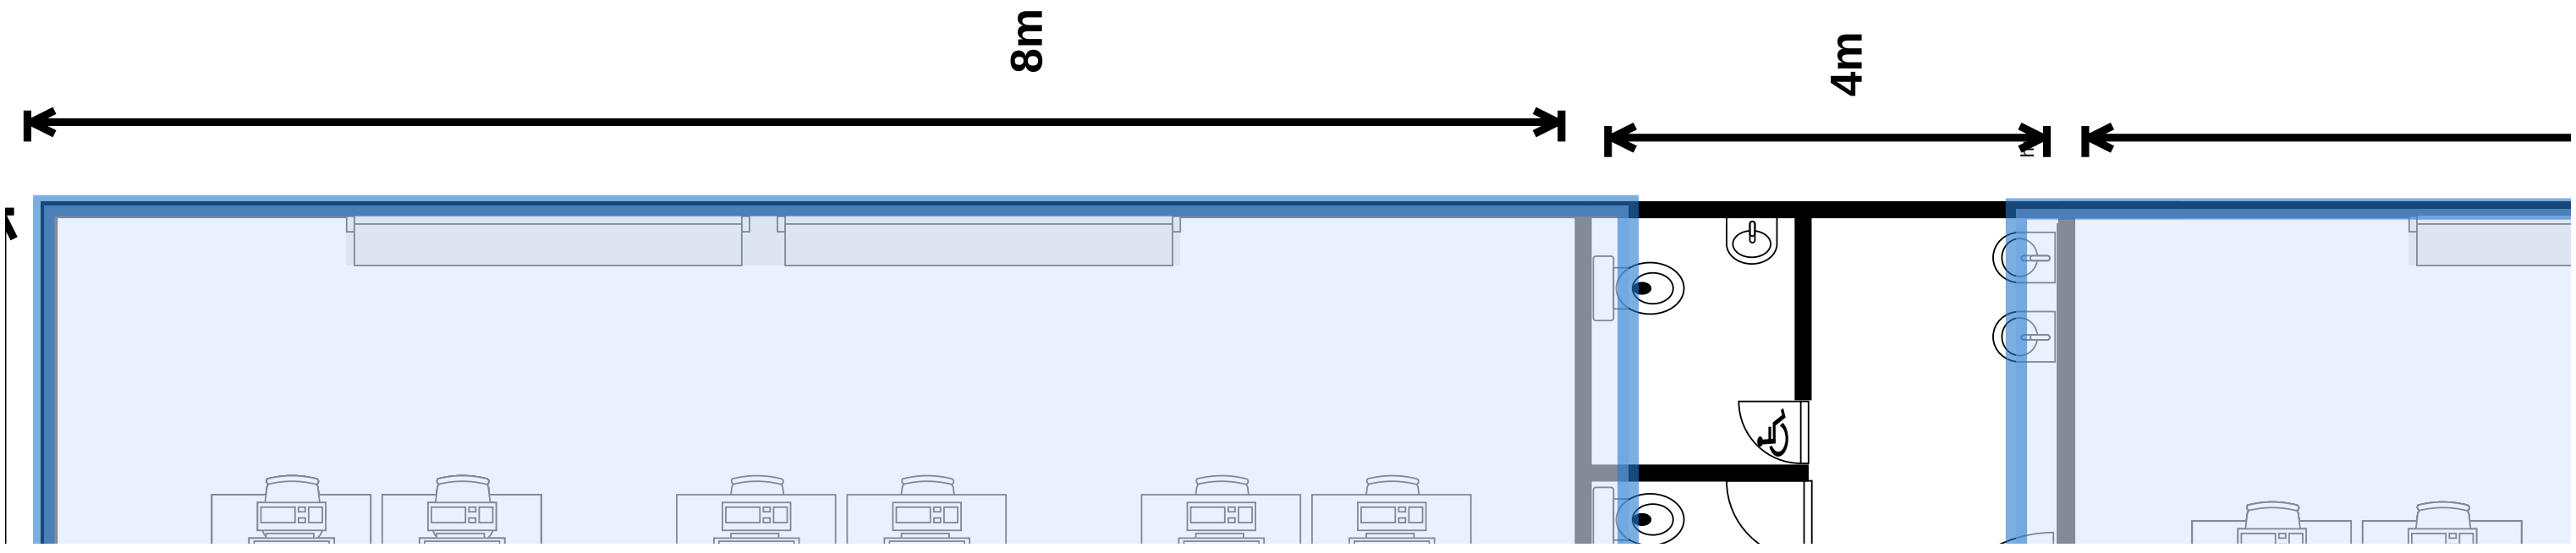

8m
ayer room

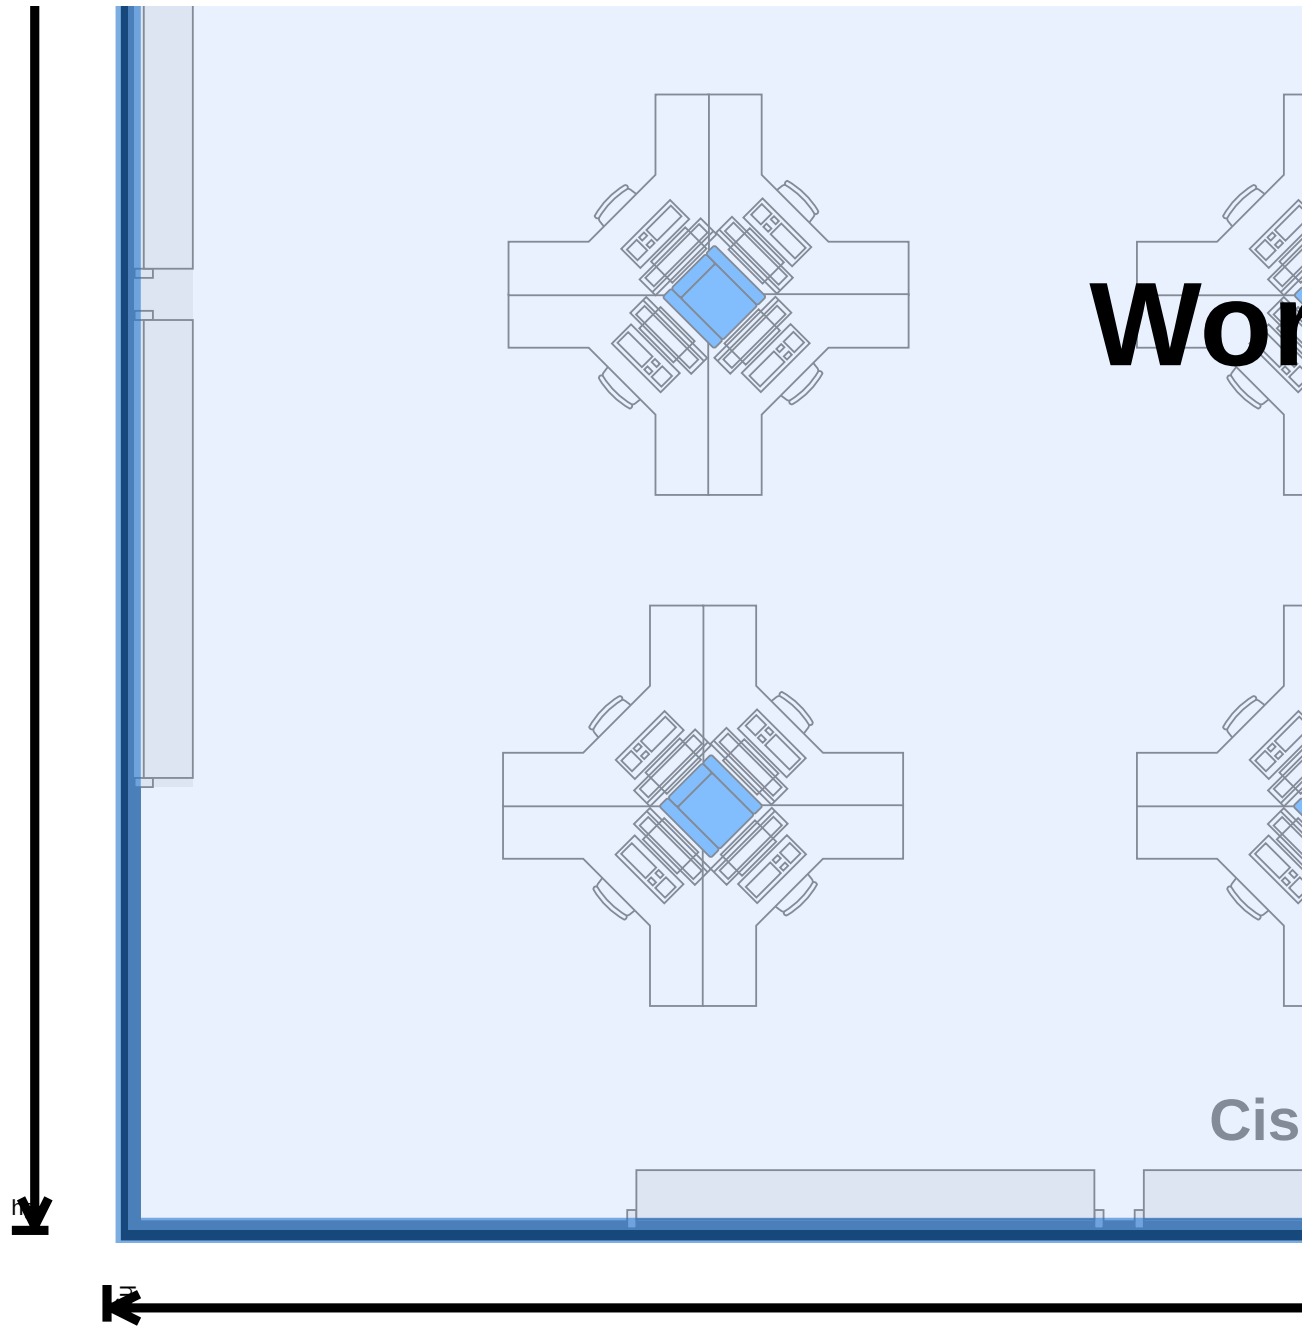

8m
4m
Work
Males bathroom

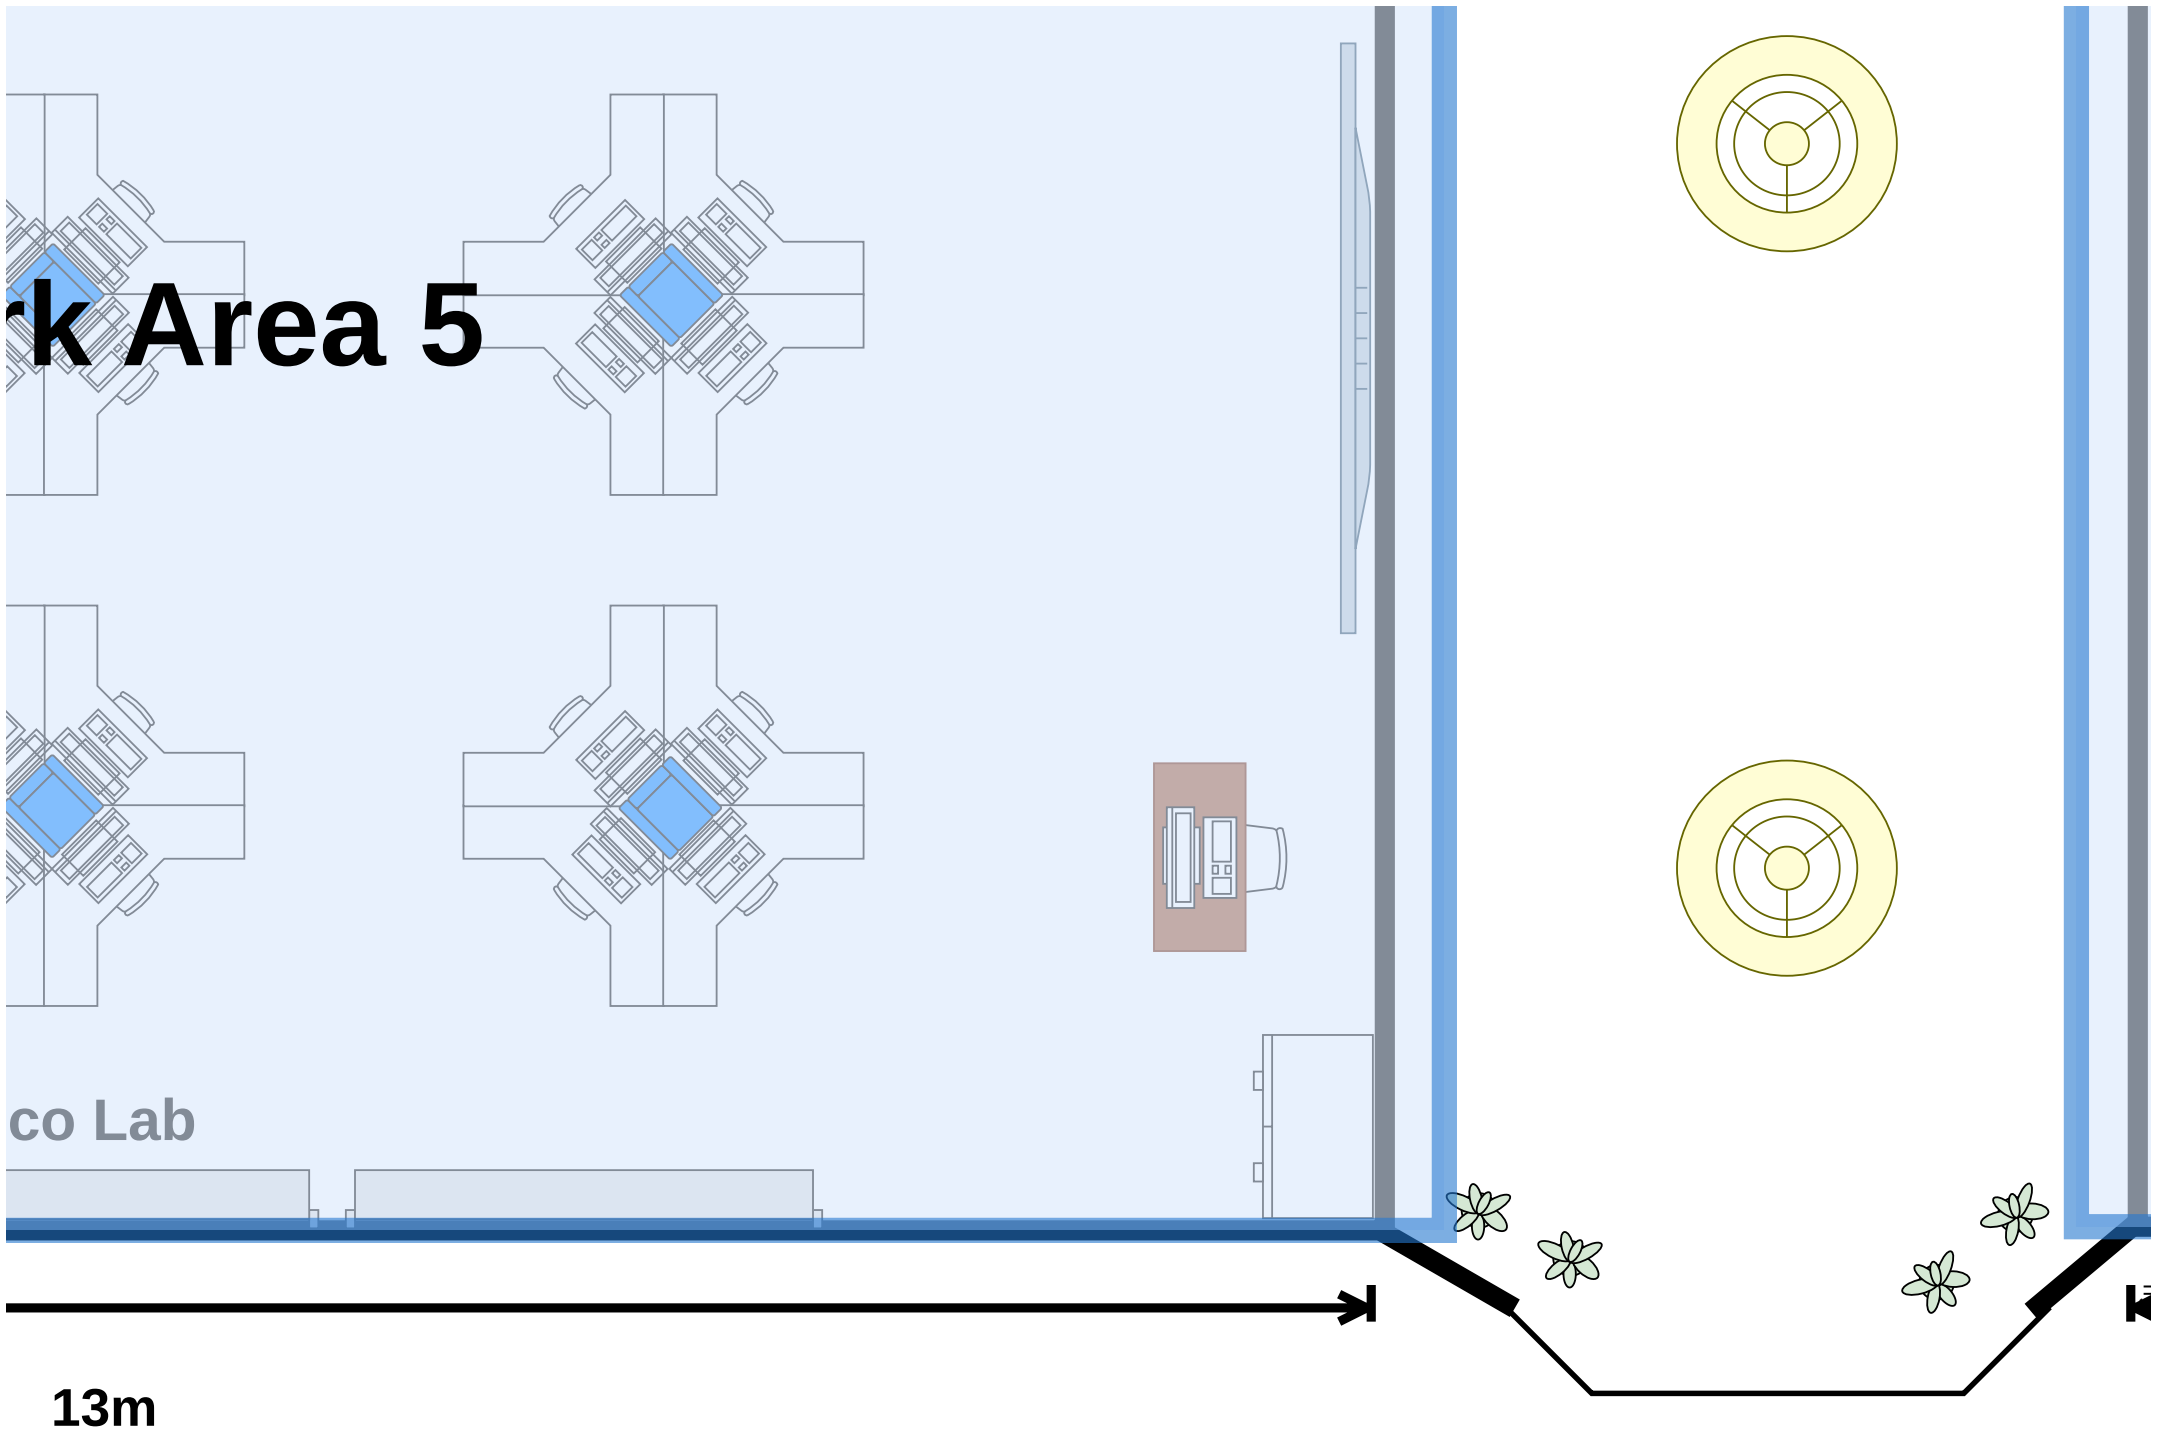
k Area 3

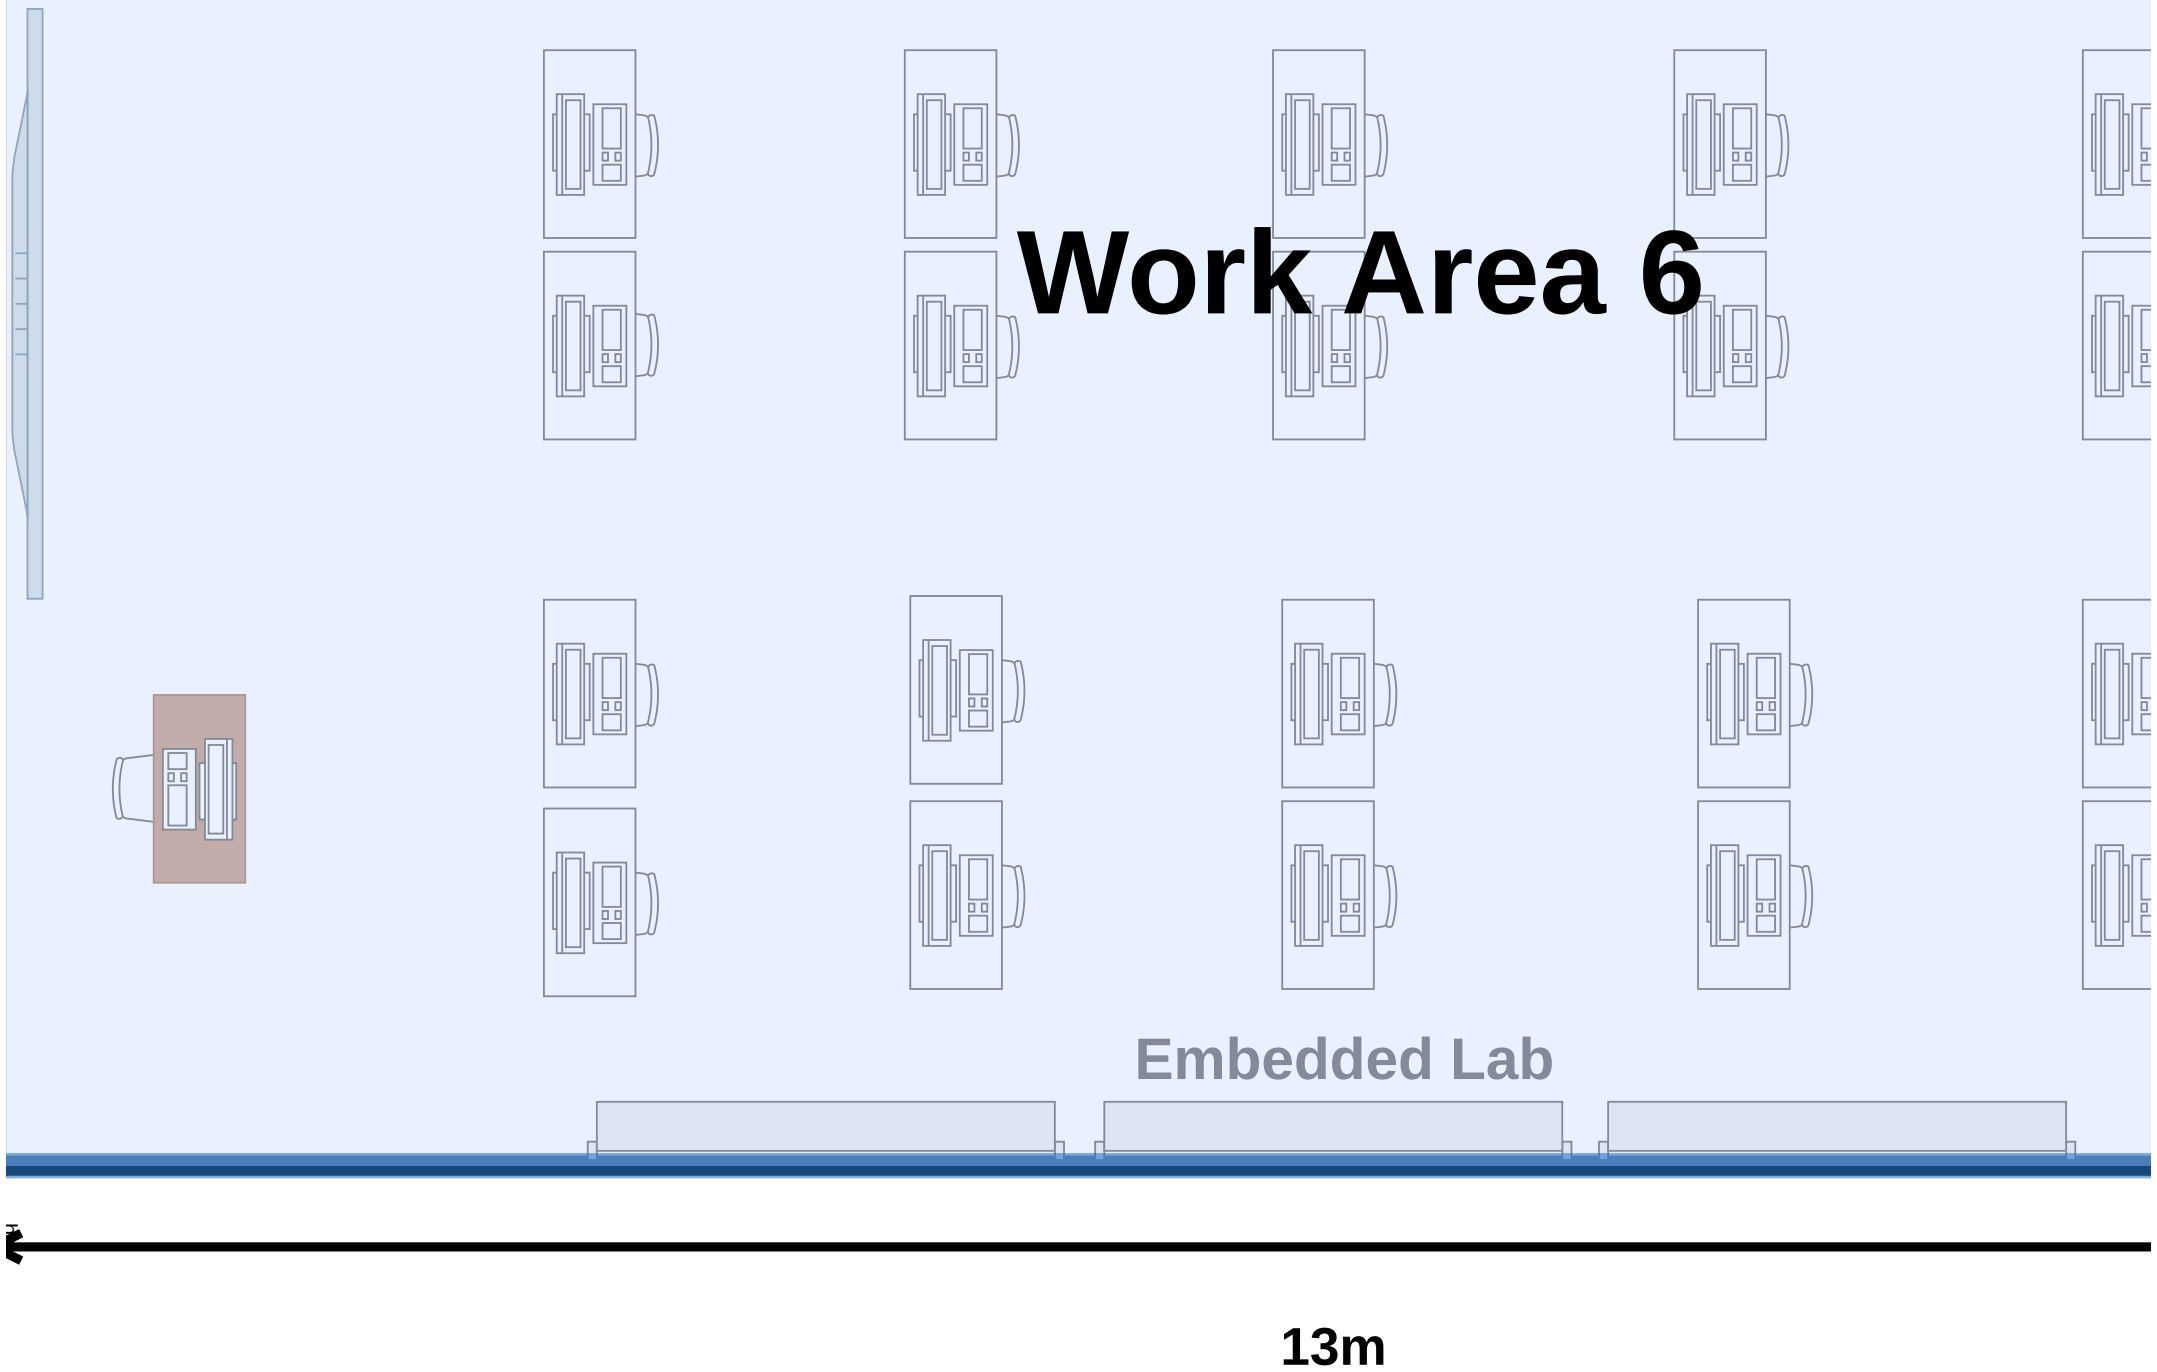
neral Lab 1

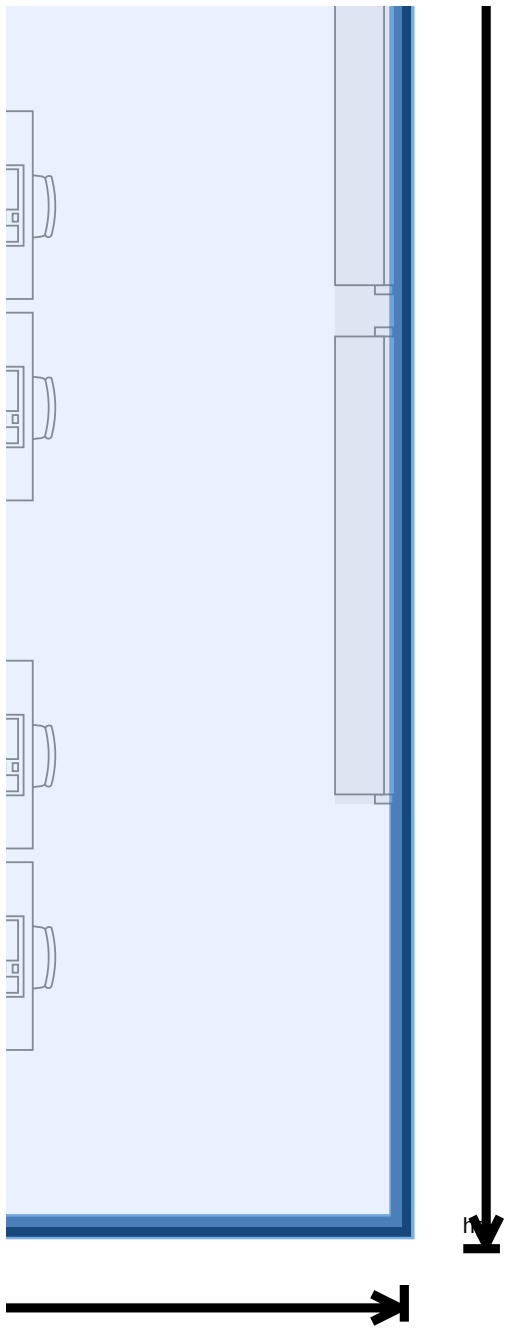

Work Area 4
General Lab 2
Females bathroom


8m
4m

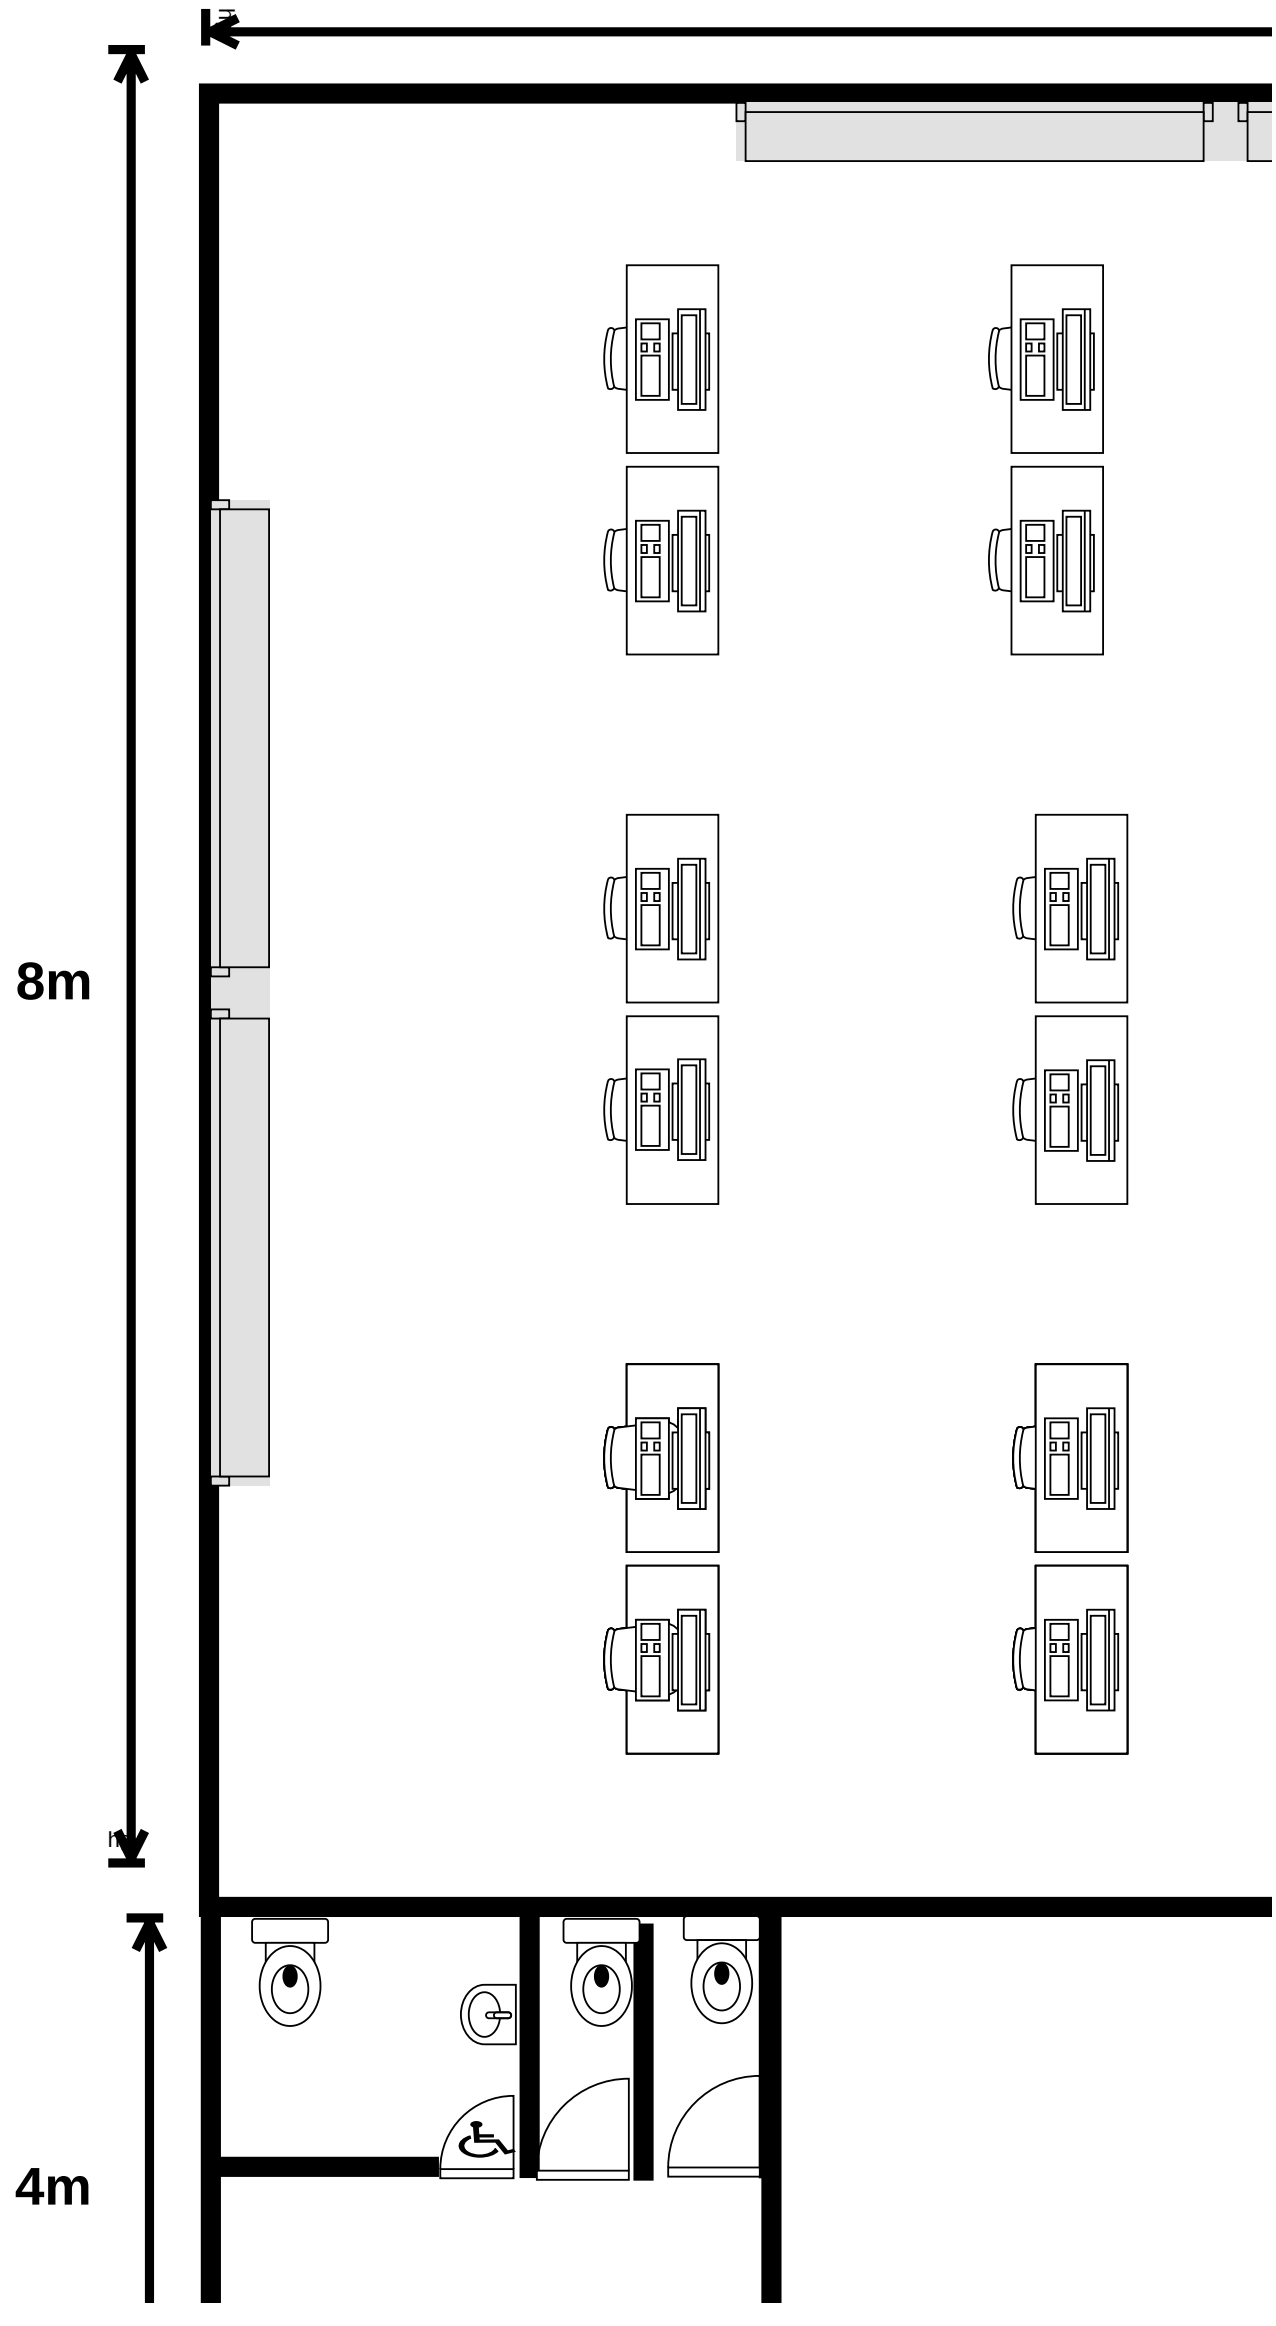

8m
Wor
Cis


rk Area 5
co Lab
13m


Work Area 6
Embedded Lab
13m


8m

Connected Devices



Second Floo

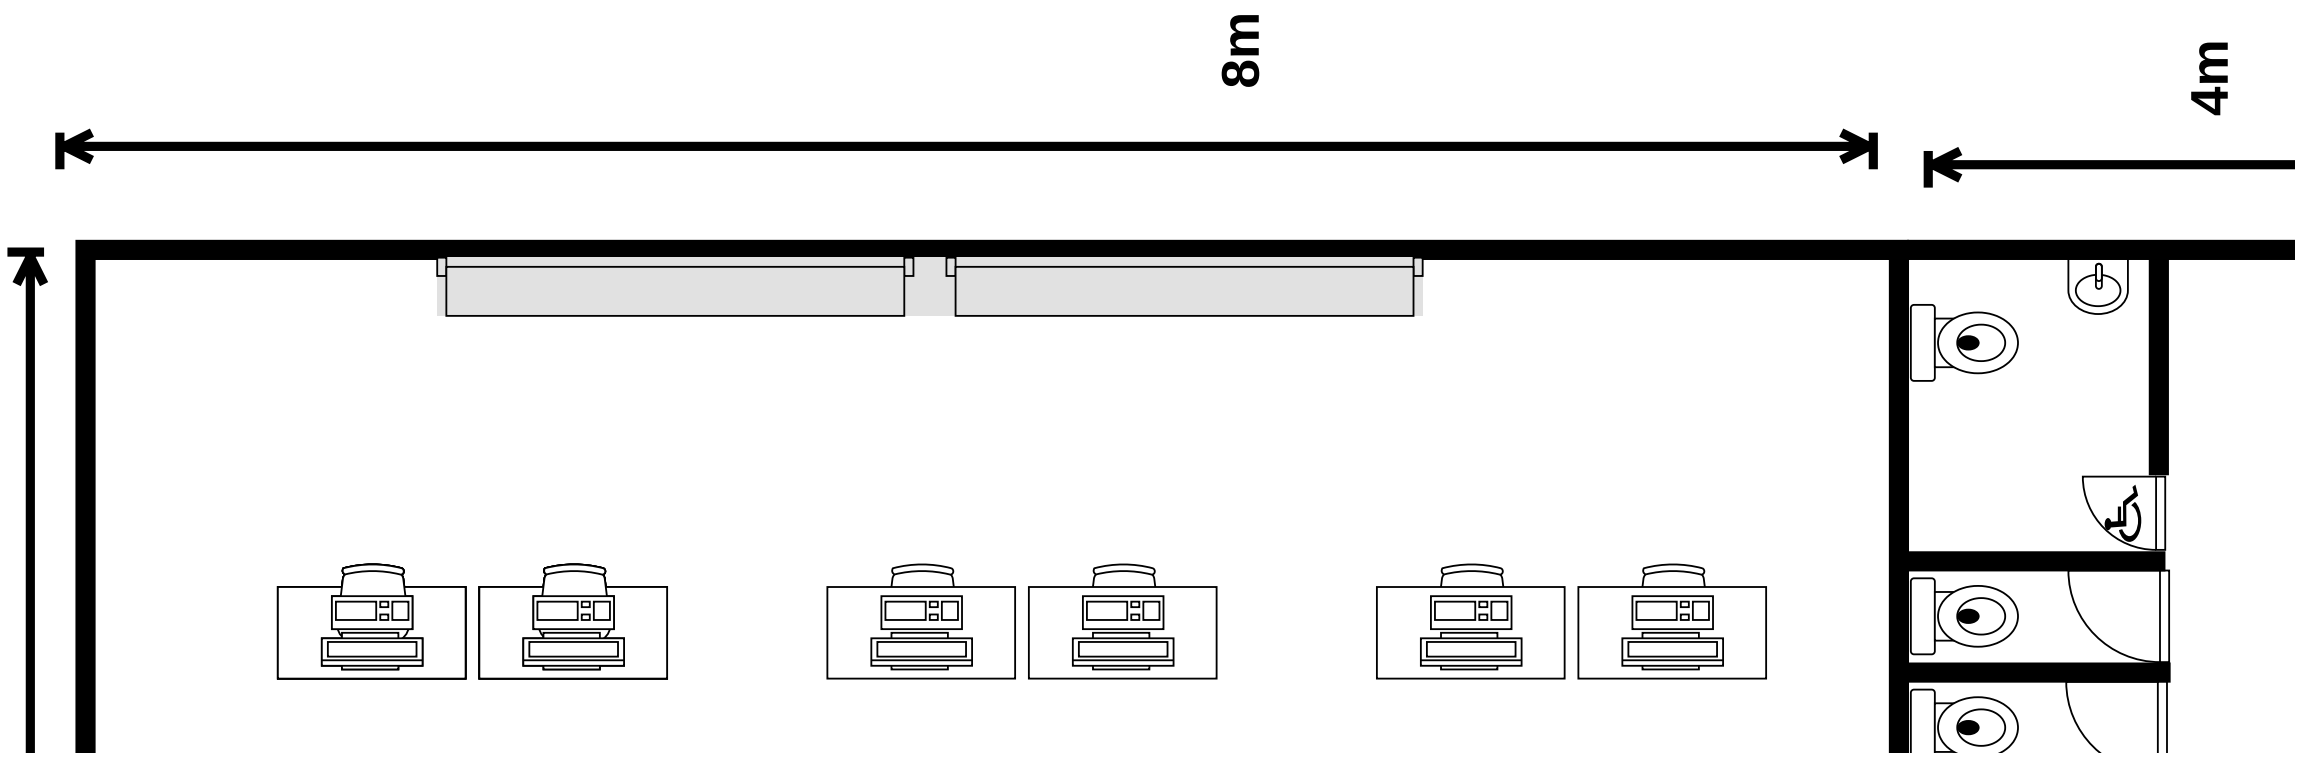
13m

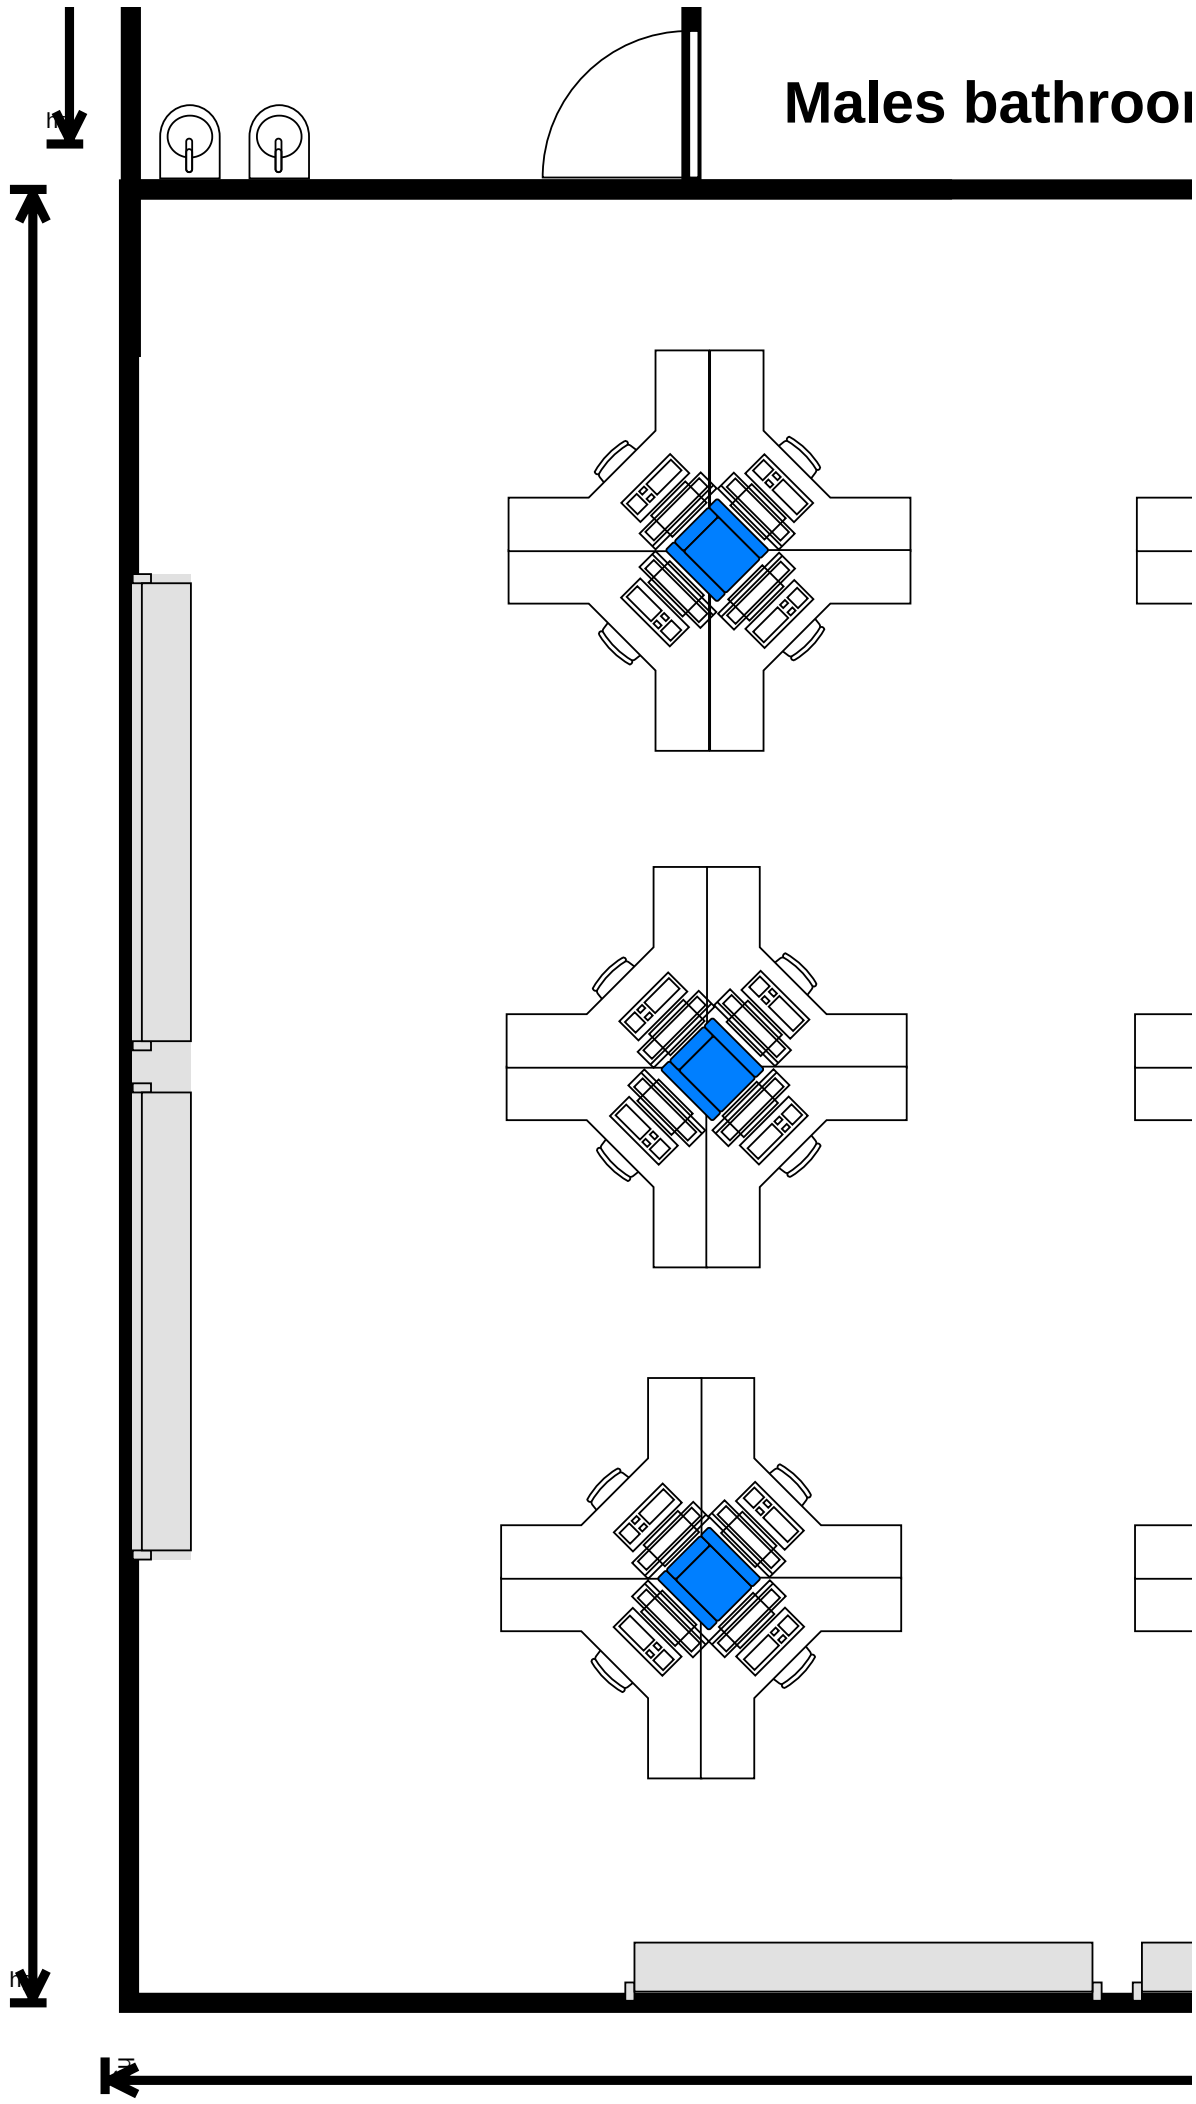
General Lab 1

r

13m

General Lab 2

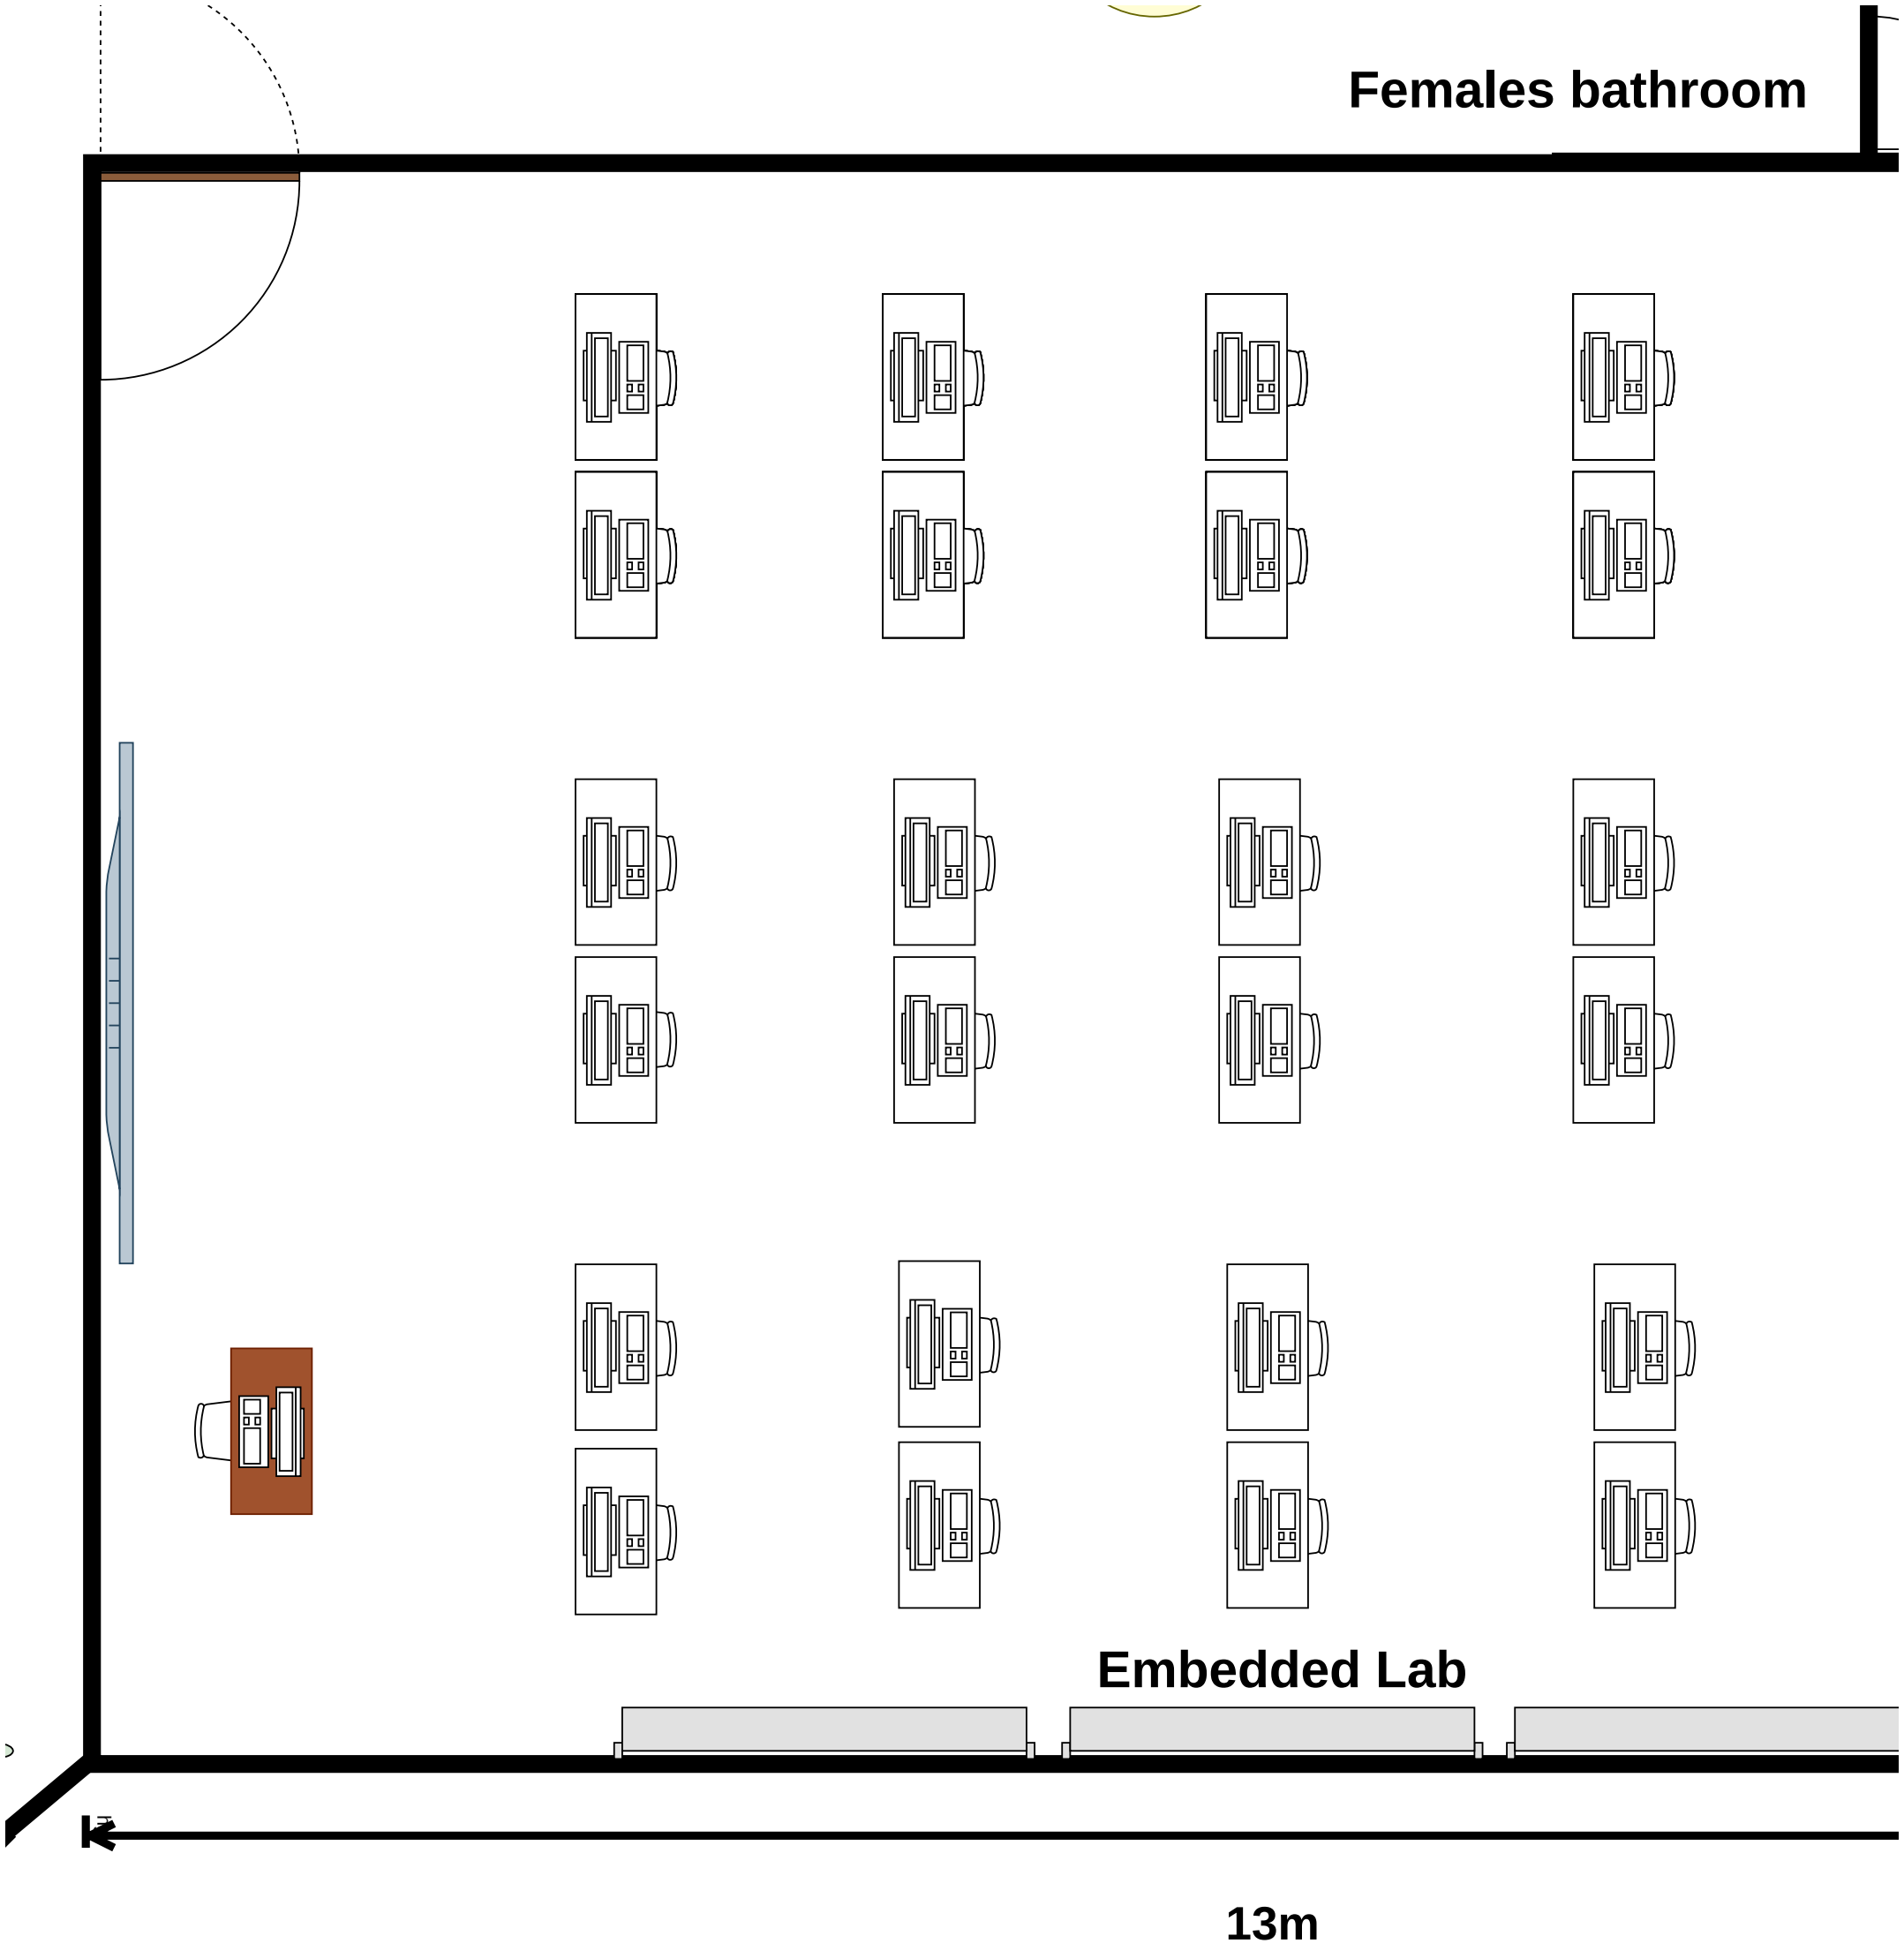

8m
4m

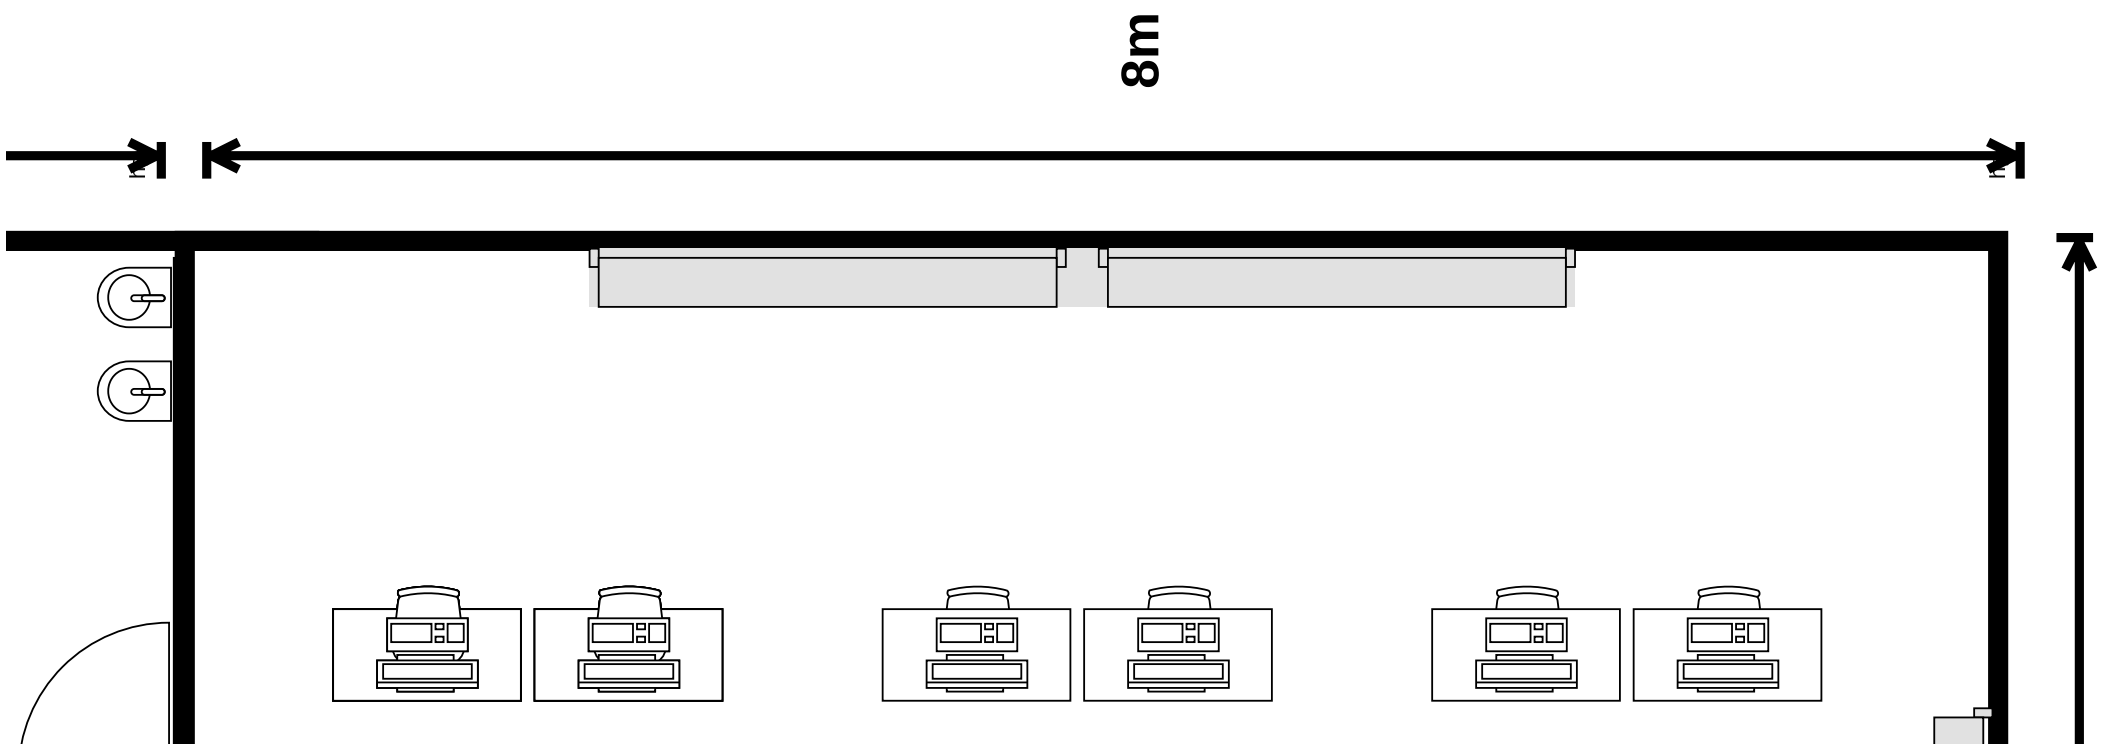

Males bathroo
8m

m

Cisco Lab

13m


Females bathroom
Embedded Lab
13m


8m